



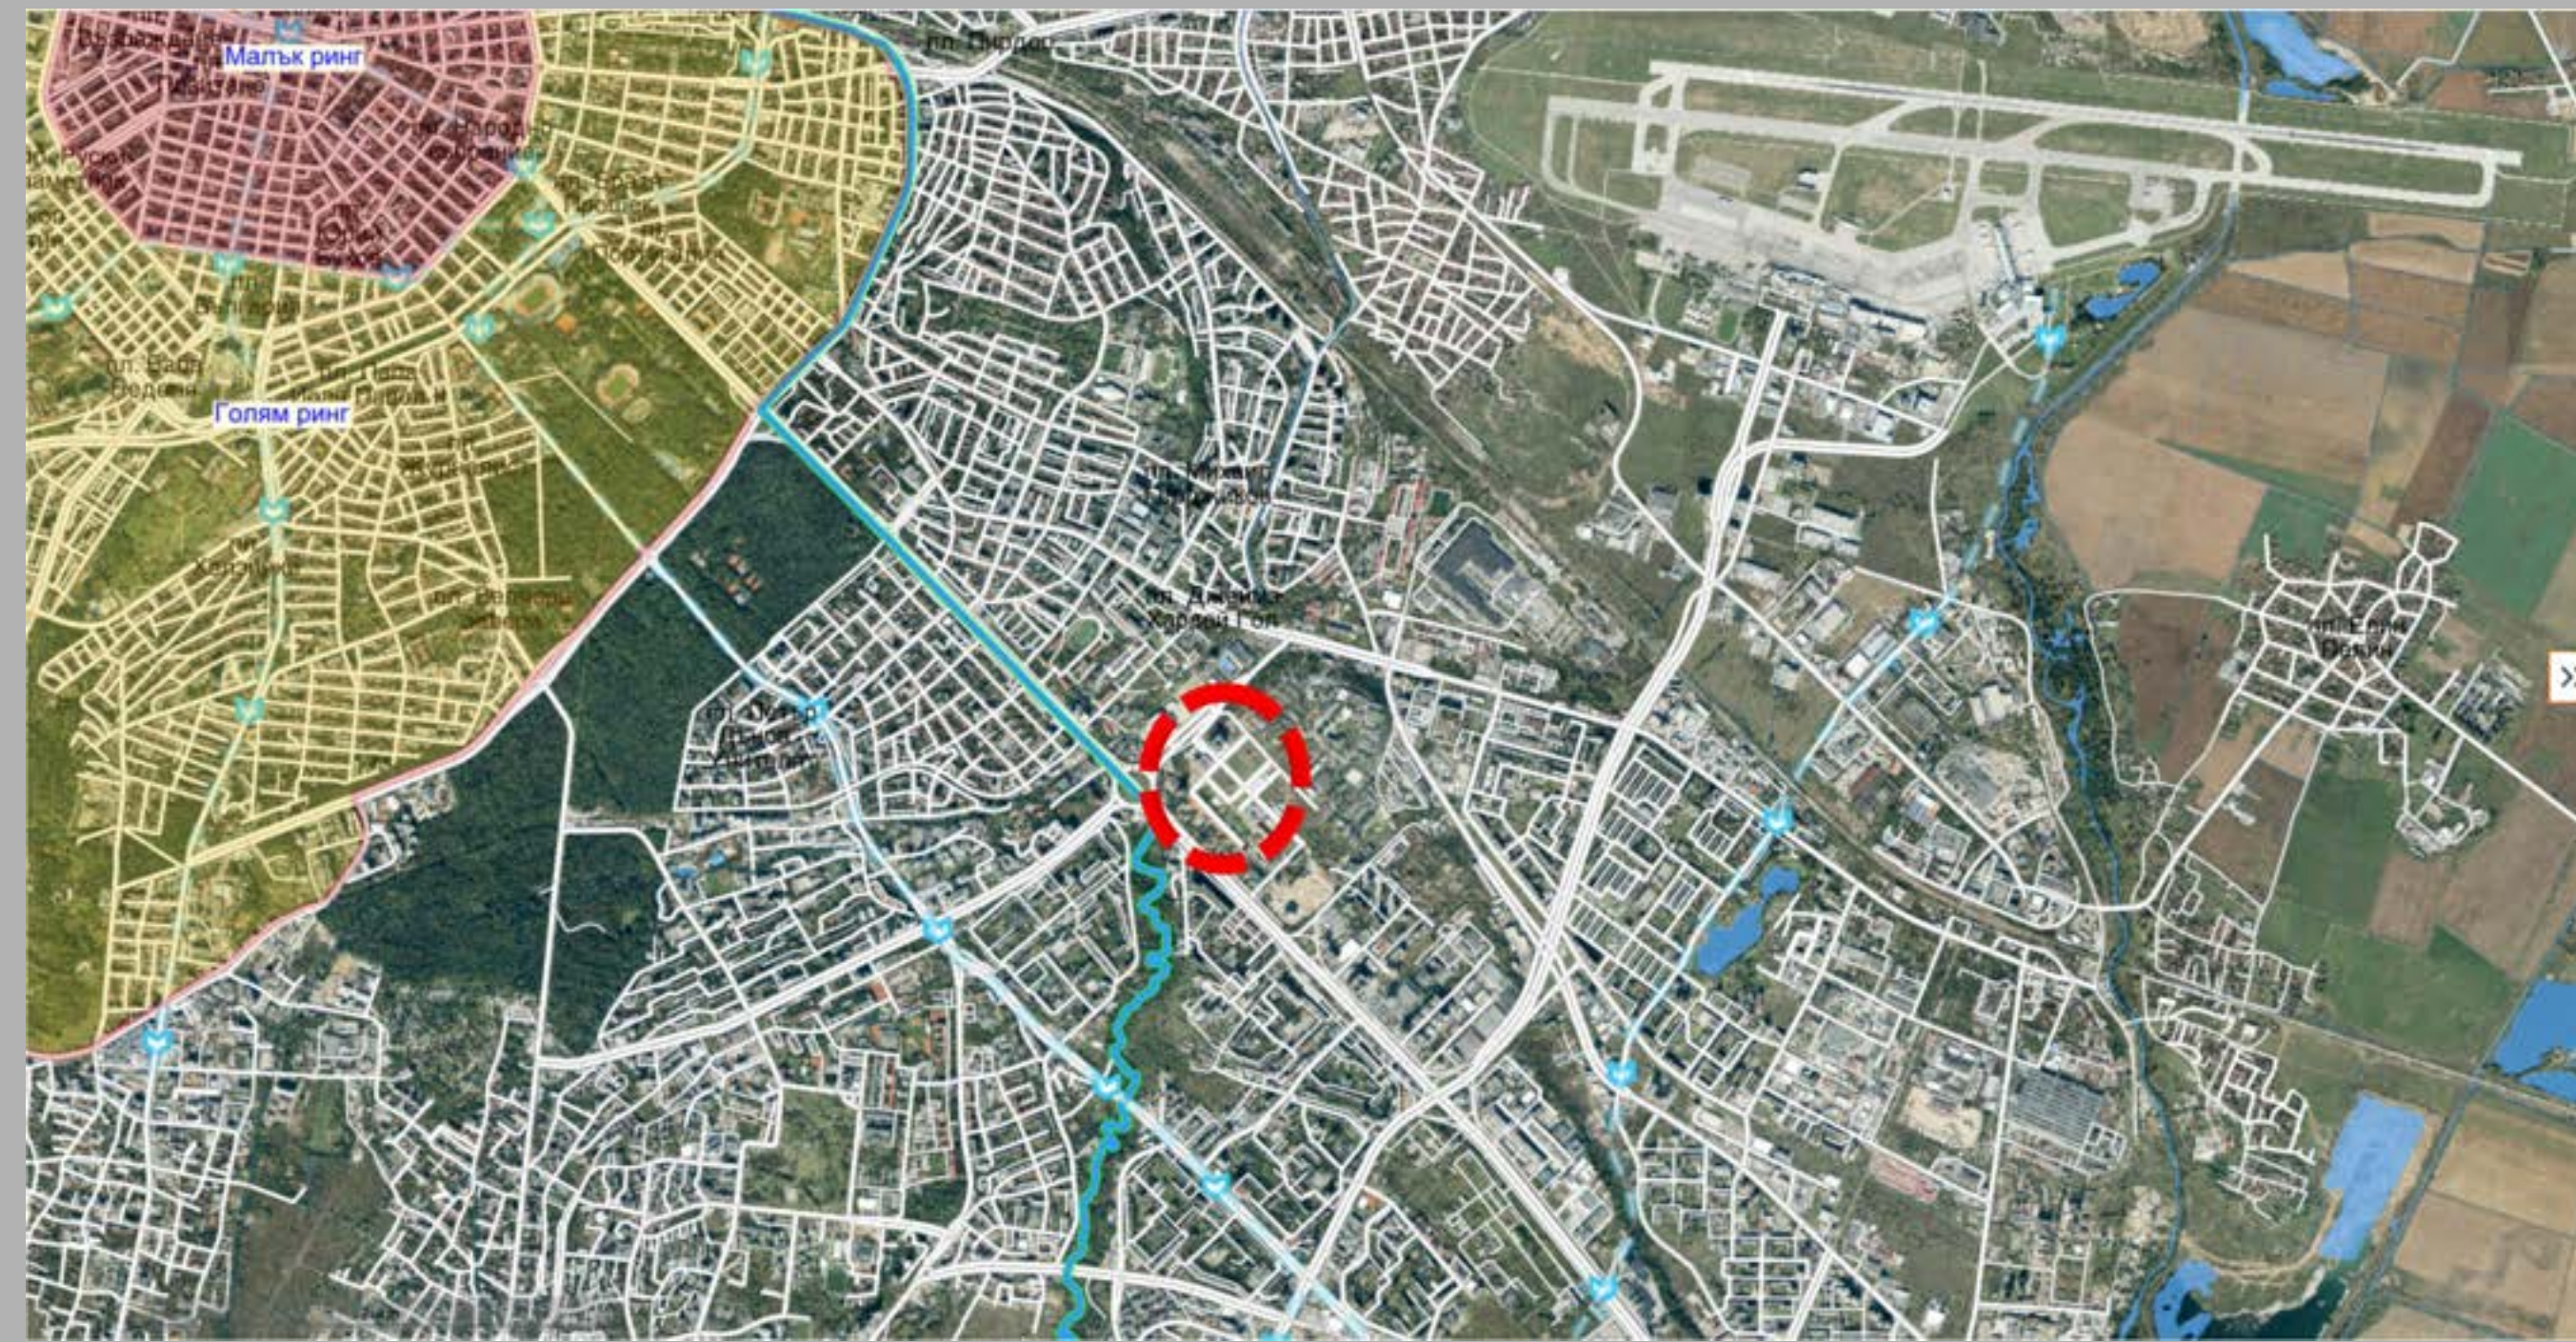




СХЕМА: КОМУНИКАЦИИ И ТРАНСПОРТНИ ВРЪЗКИ




СХЕМА: СИТУИРАНЕ НА ТЕРЕНА

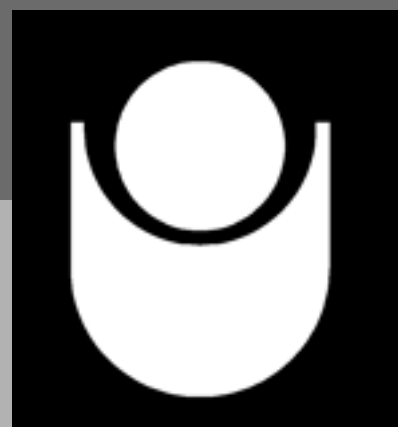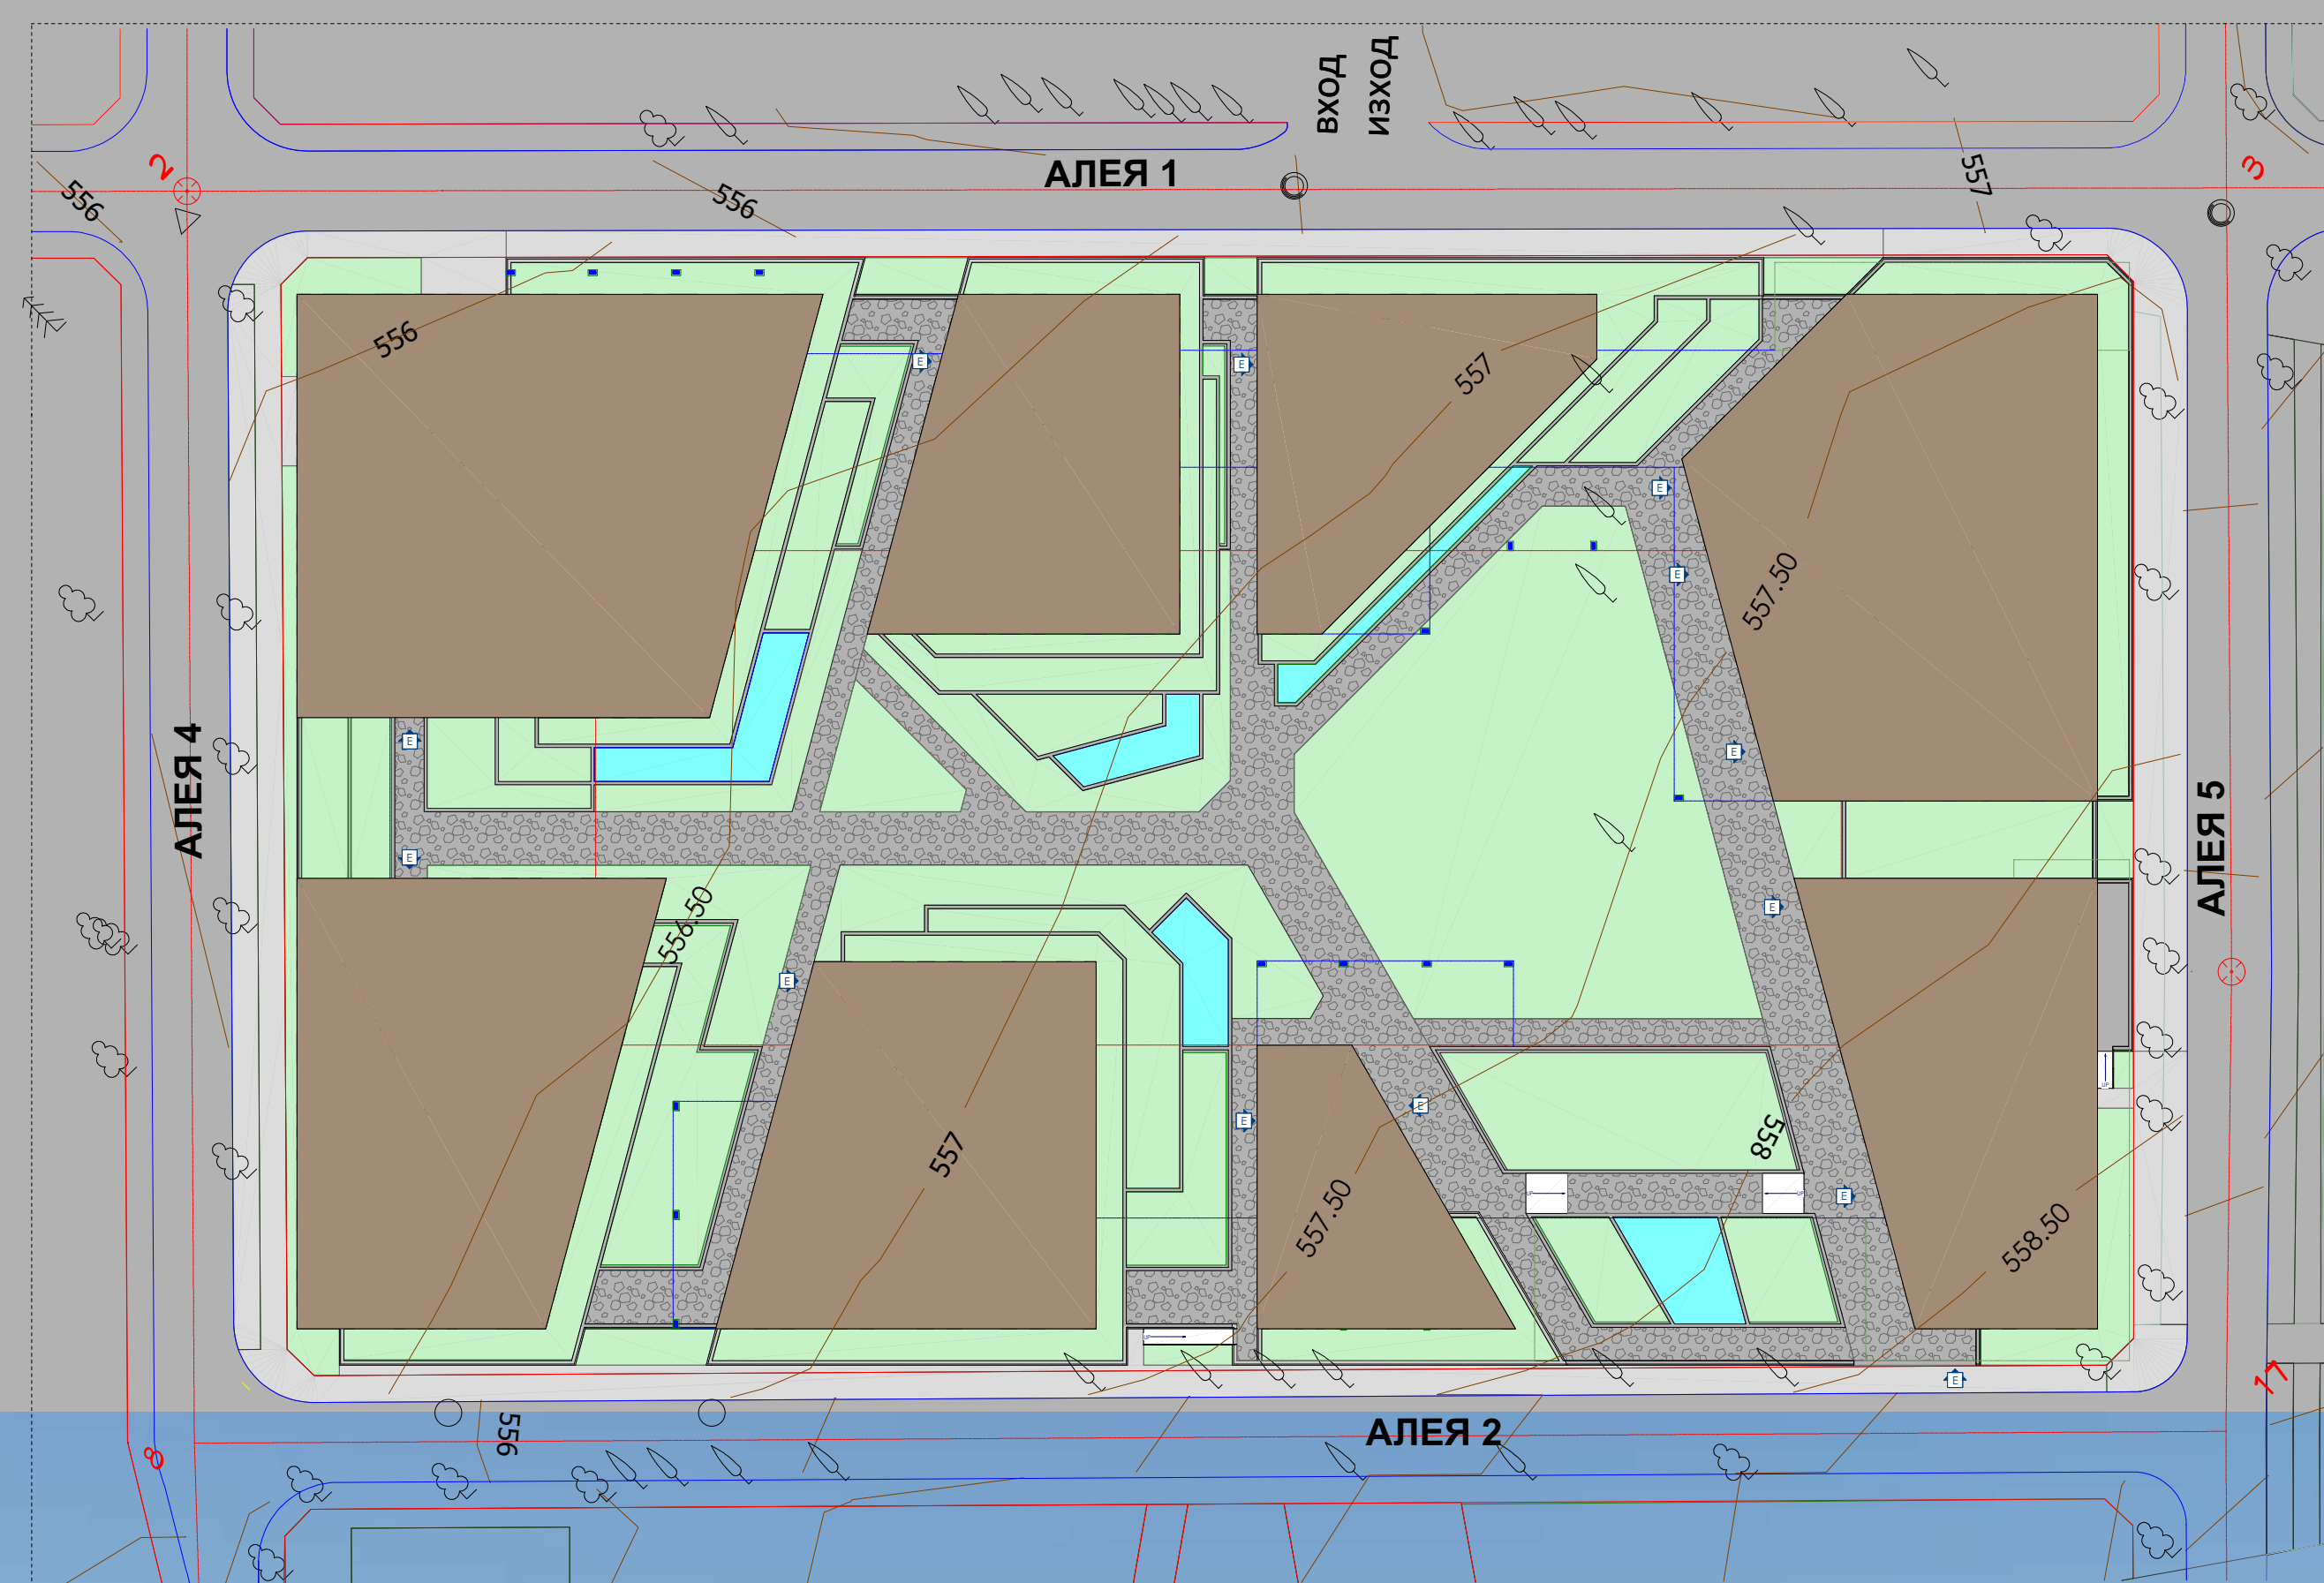


СИТУАЦИЯ М1:500

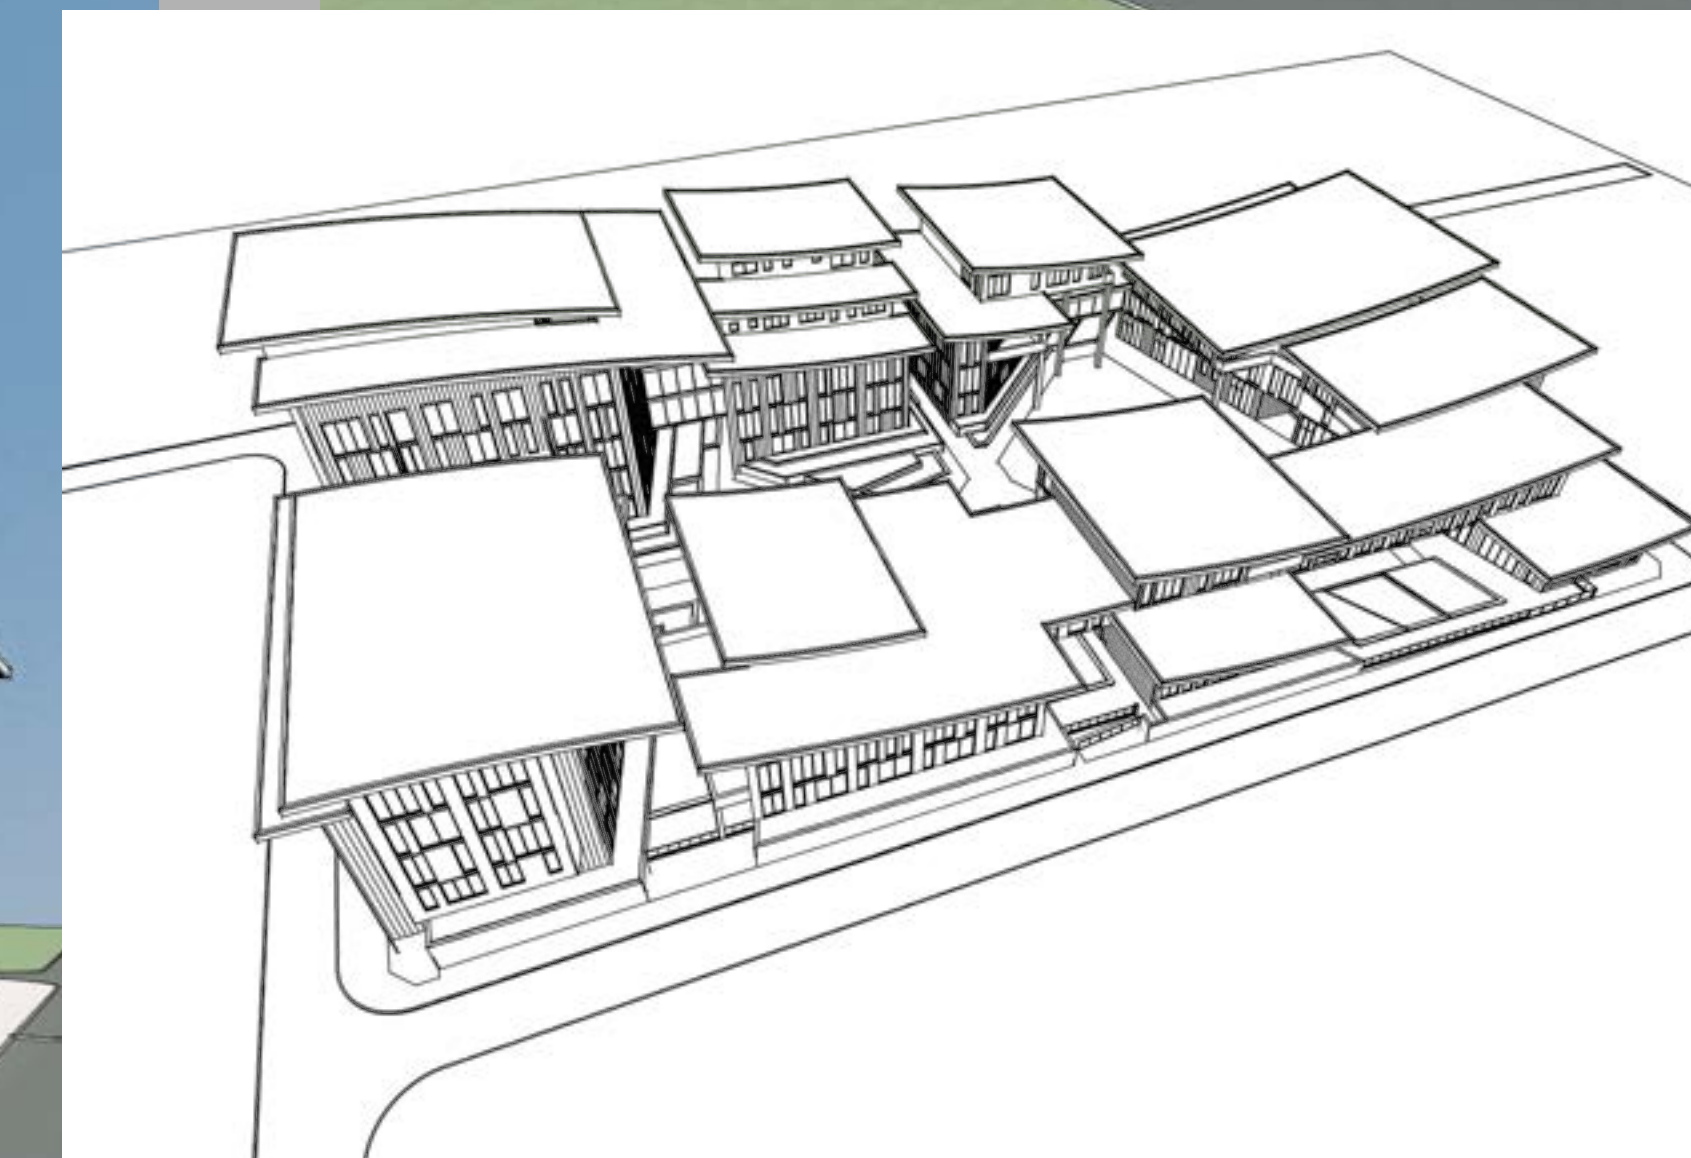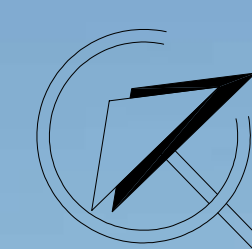



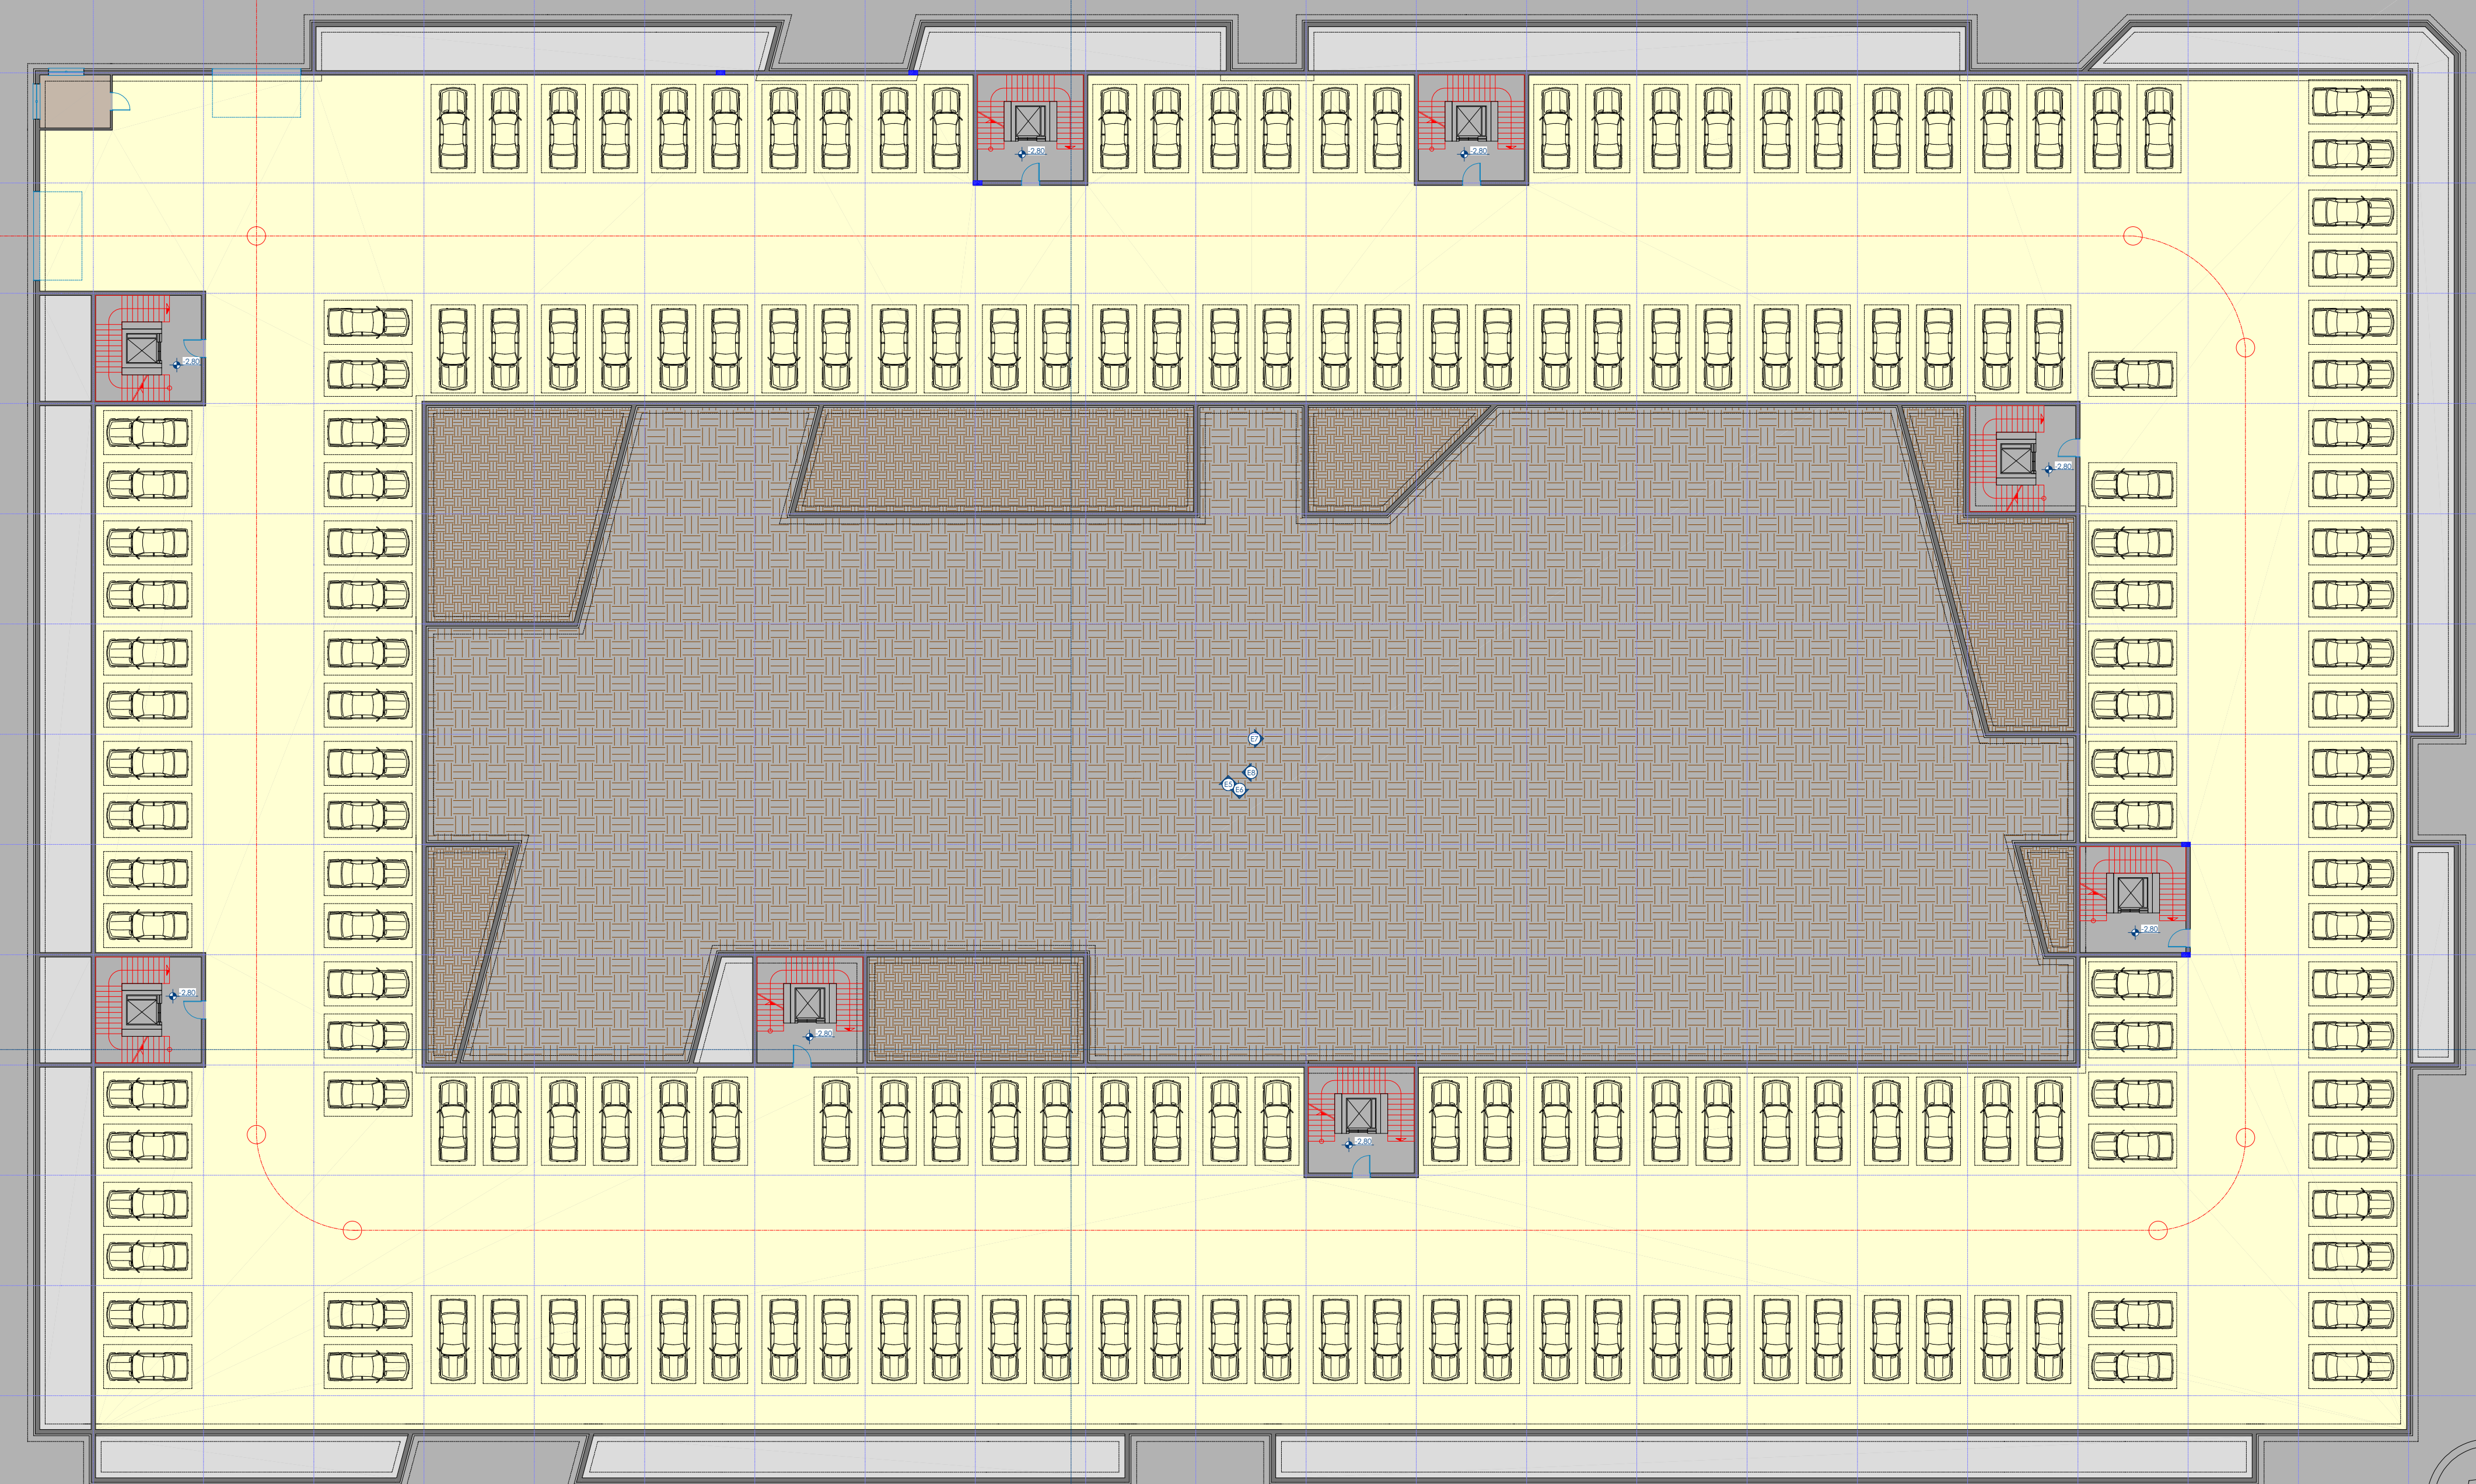



РАЗПРЕДЕЛЕНИЕ НА КОТА-2,80 М 1:250

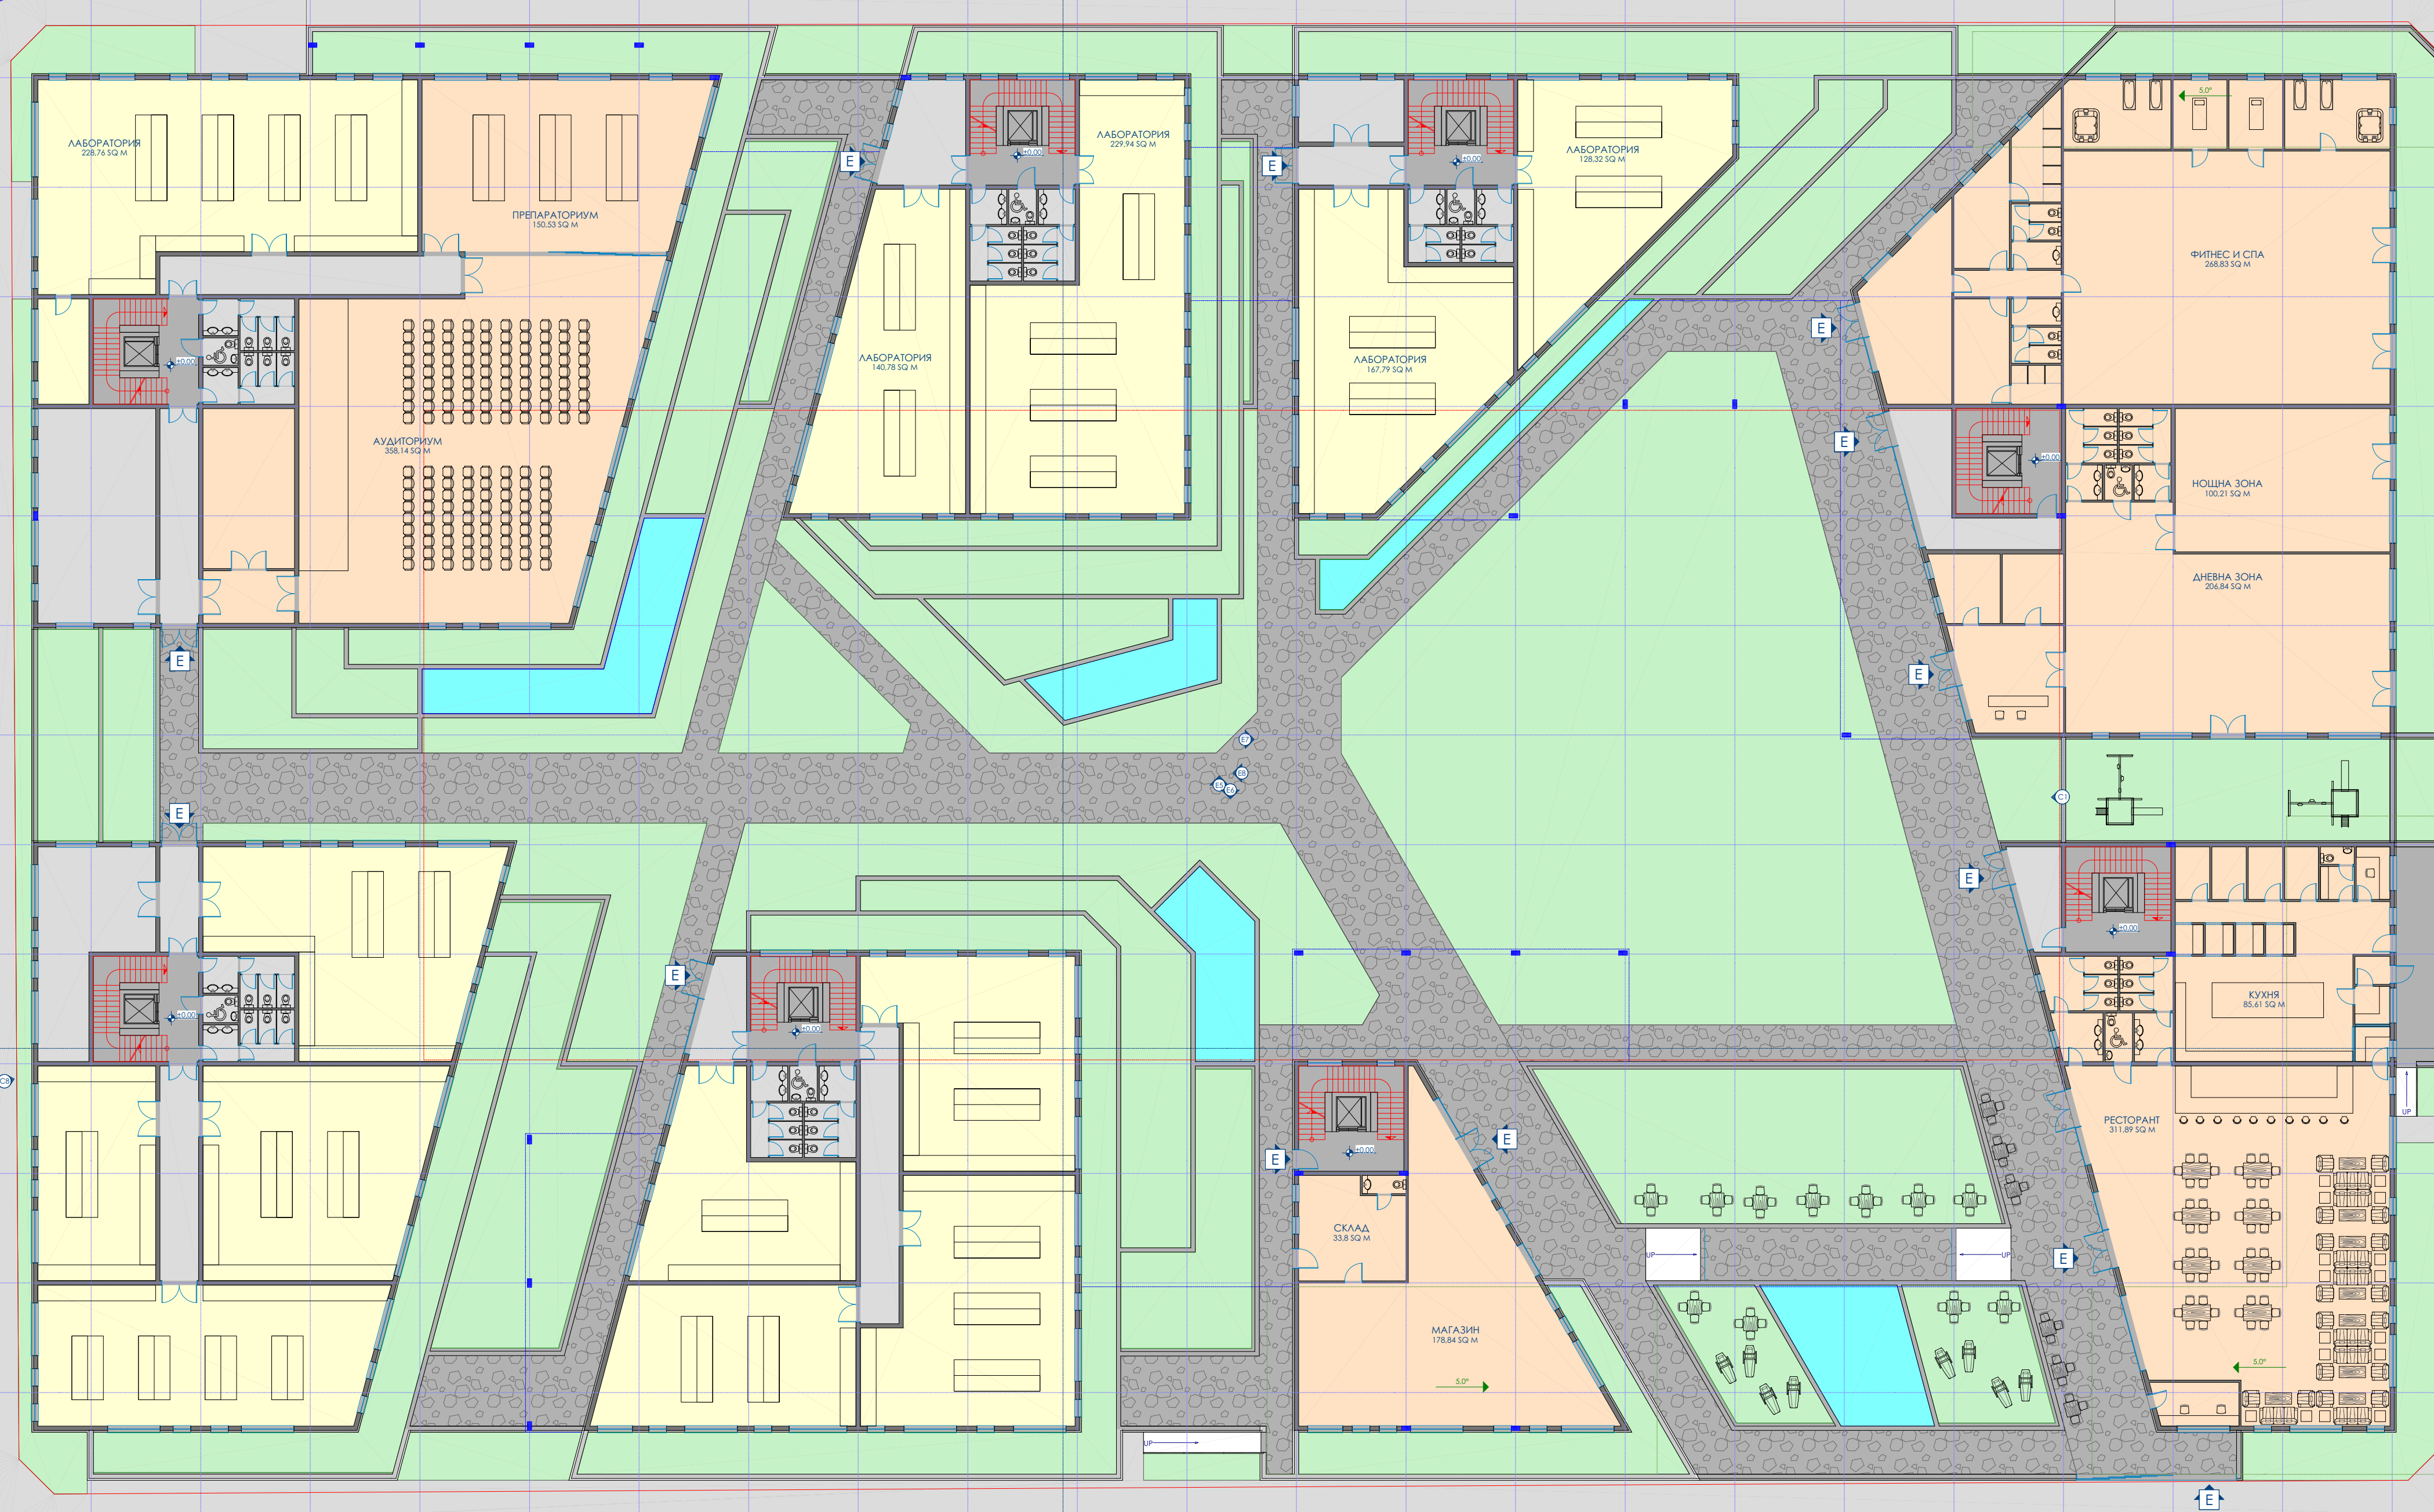


РАЗПРЕДЕЛЕНИЕ НА КОТА±0,00 М 1:250





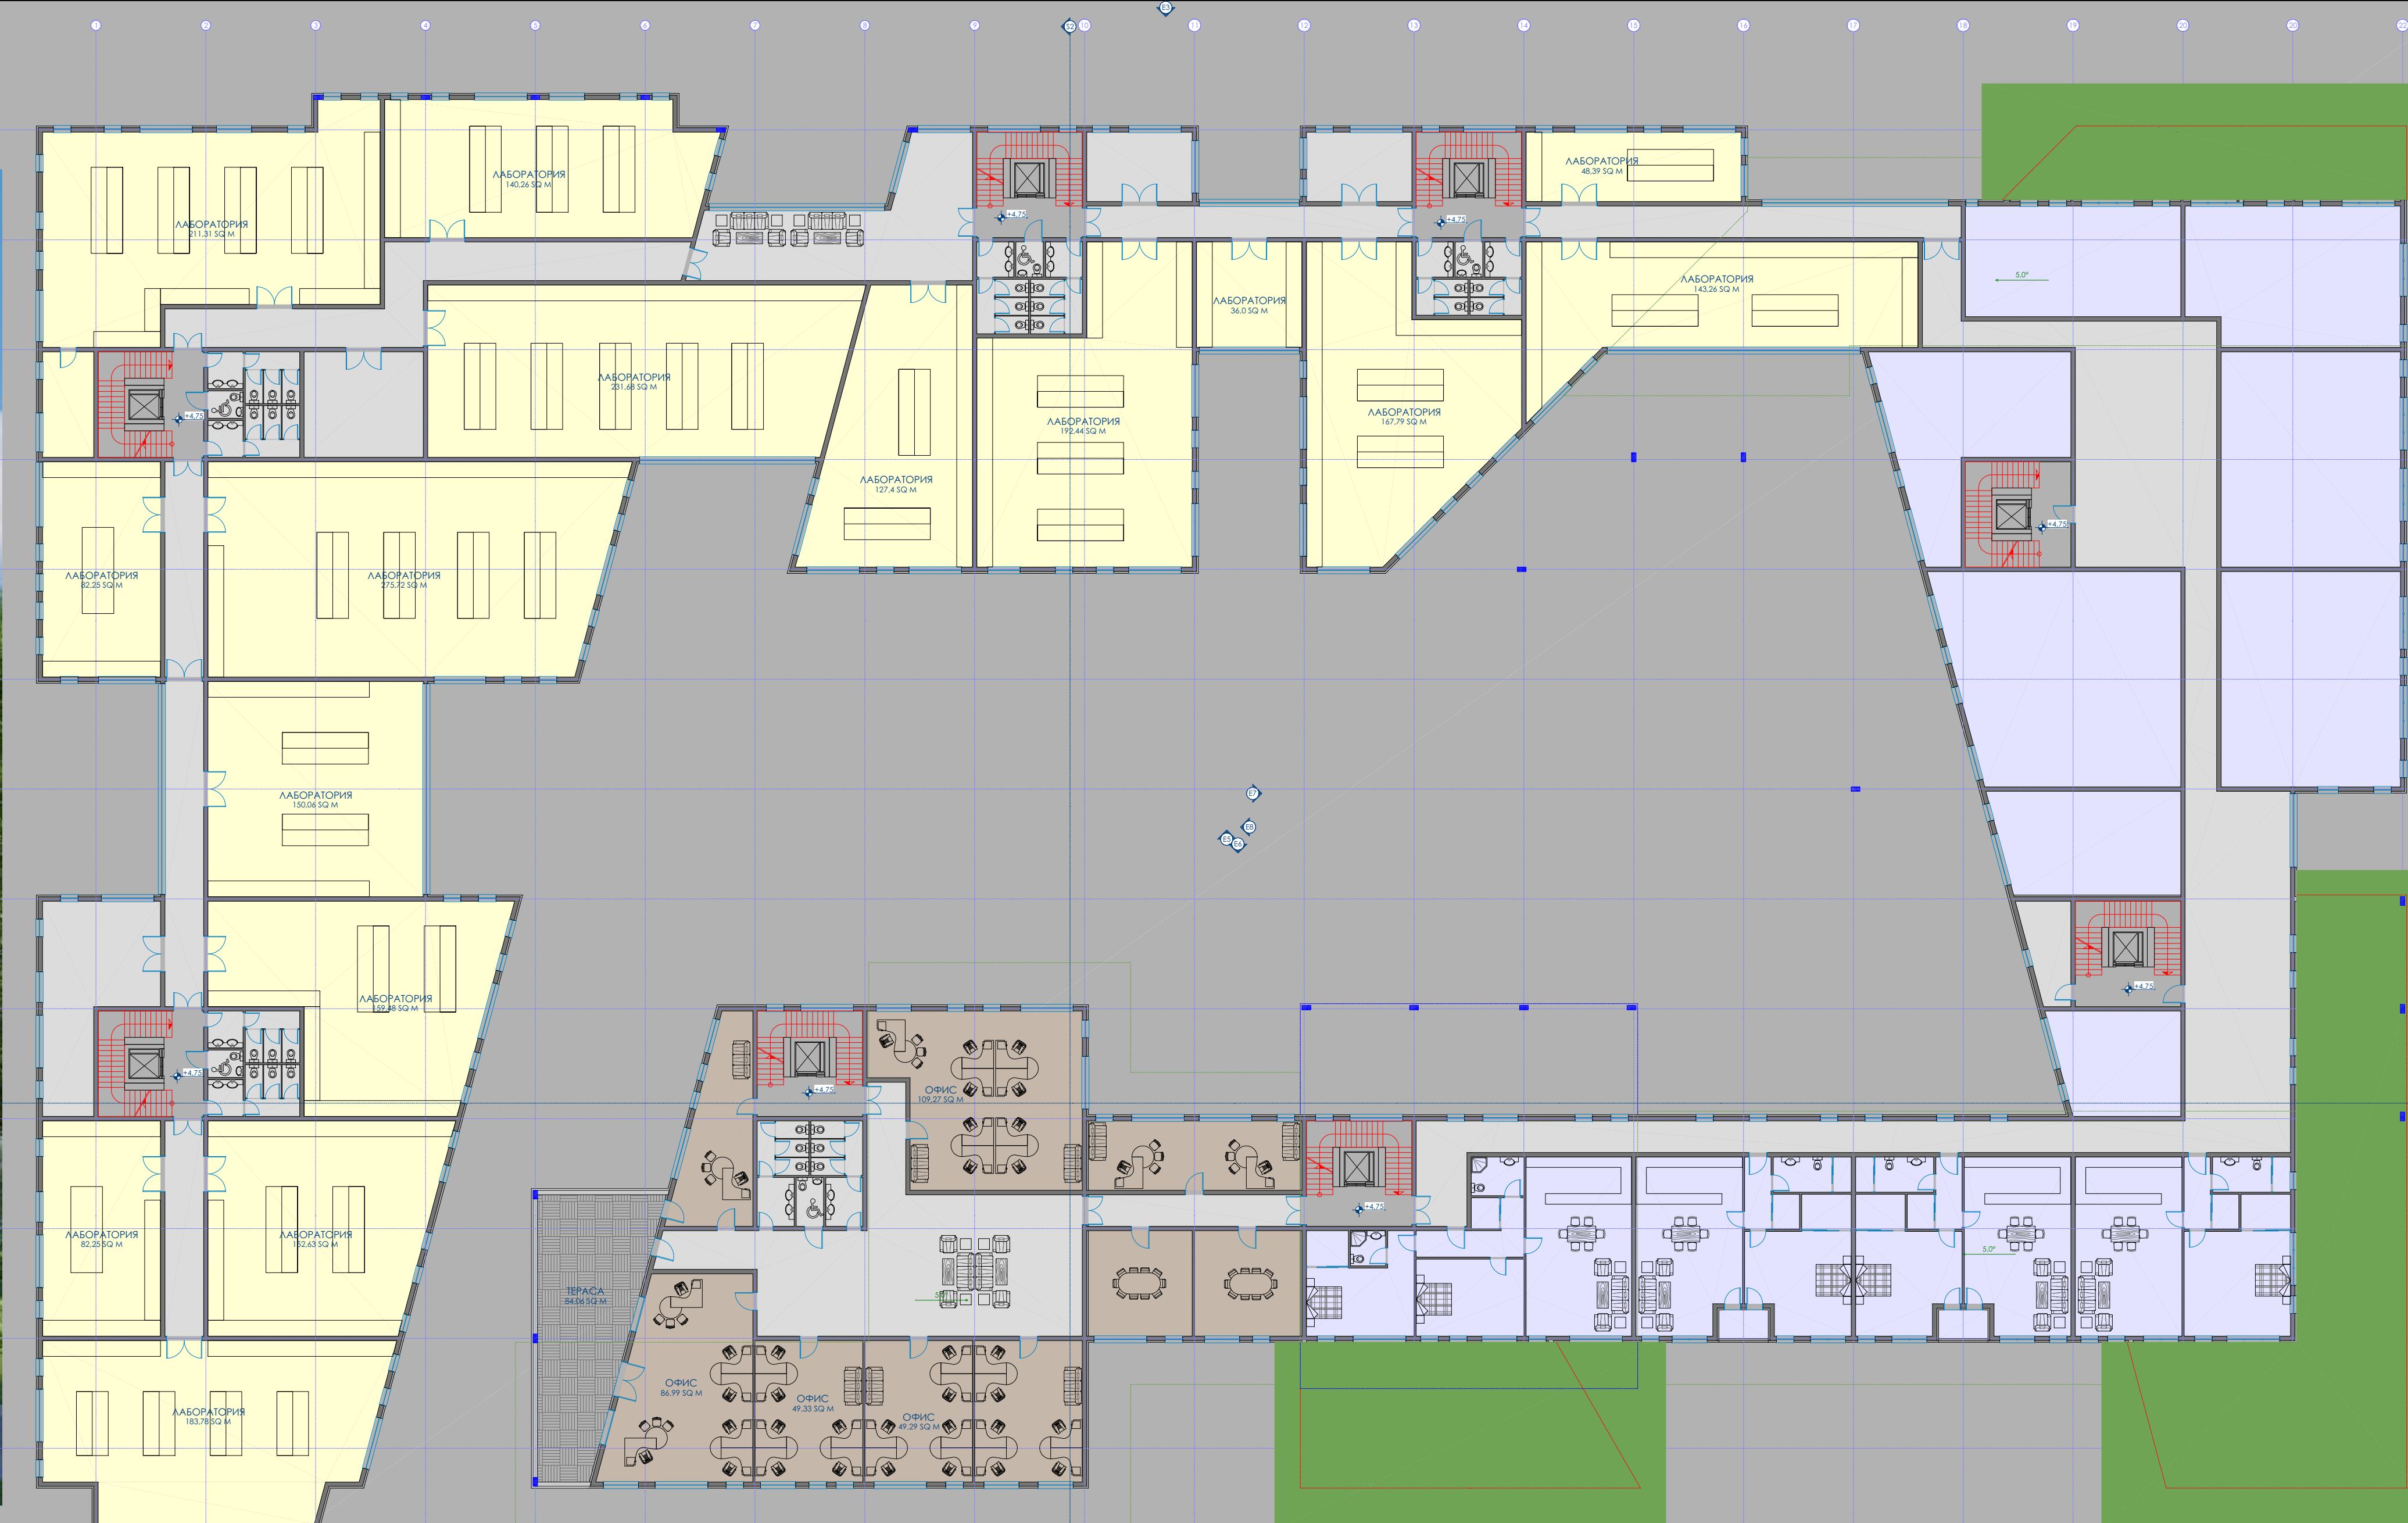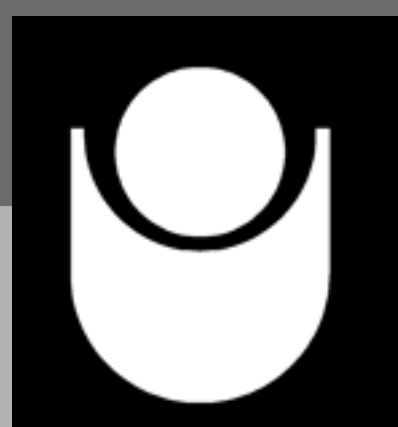


РАЗПРЕДЕЛЕНИЕ НА КОТА+4,75 М 1:250

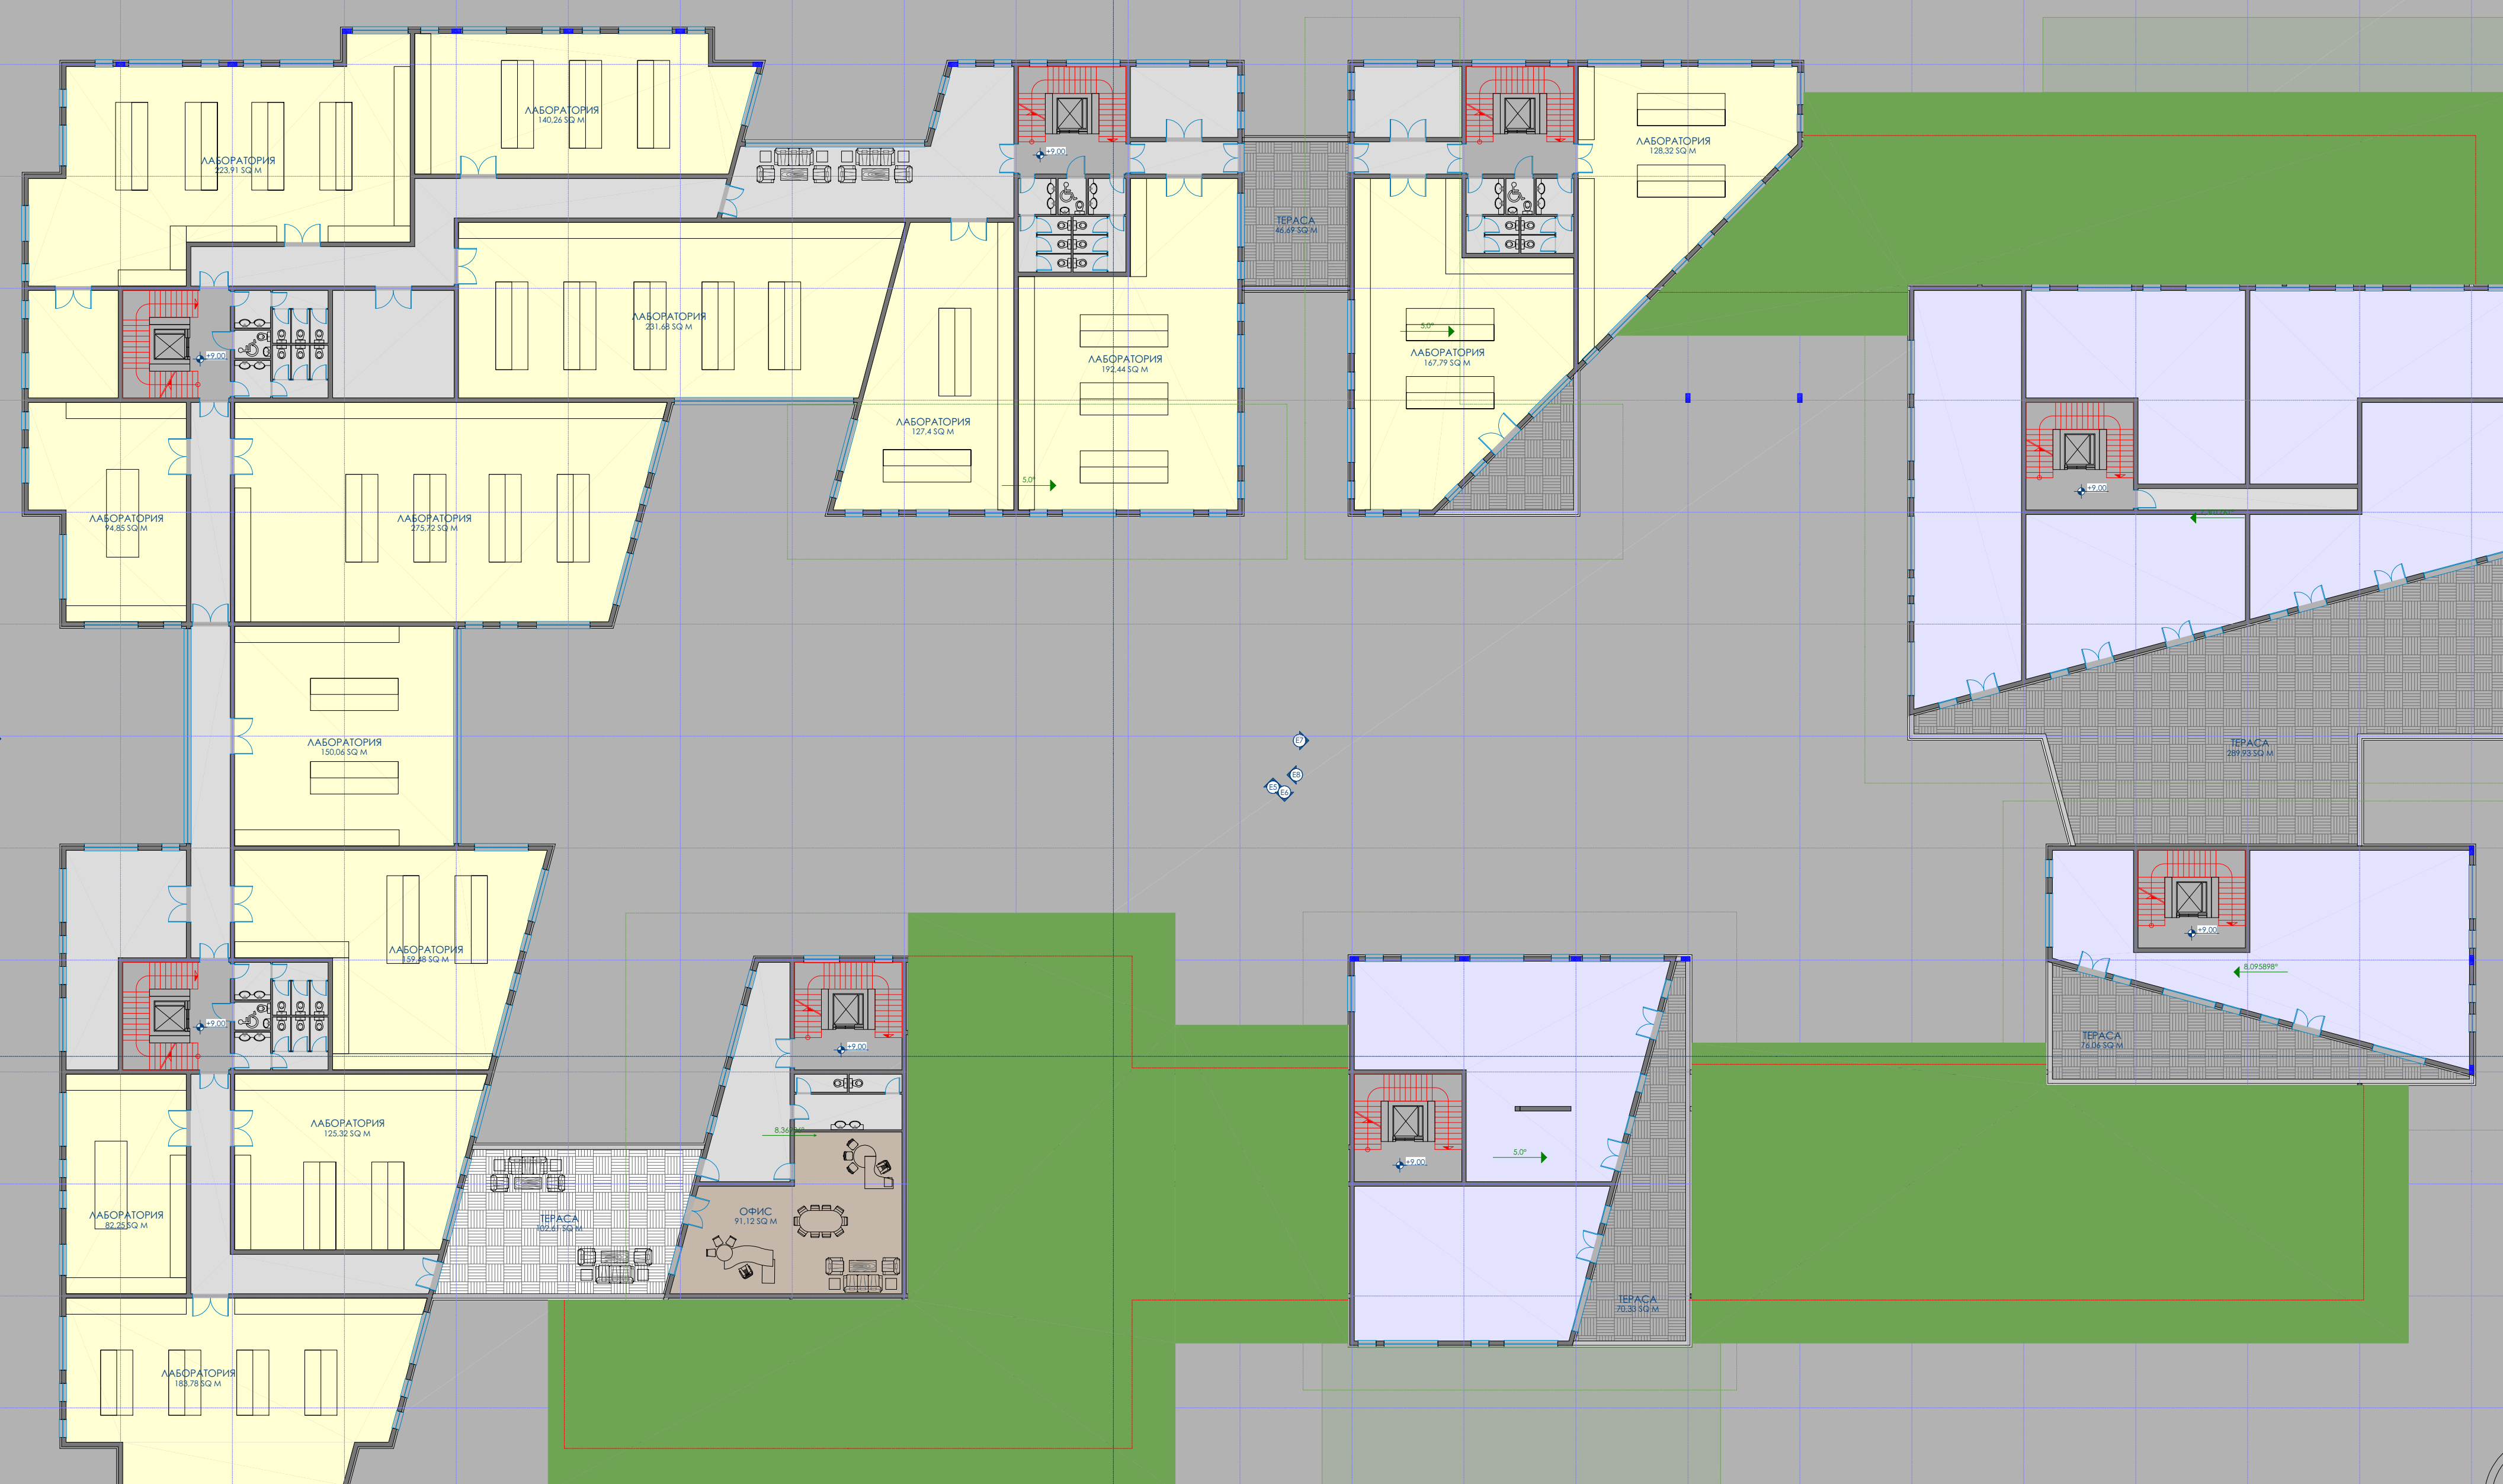


РАЗПРЕДЕЛЕНИЕ НА КОТА+9,00 М 1:250





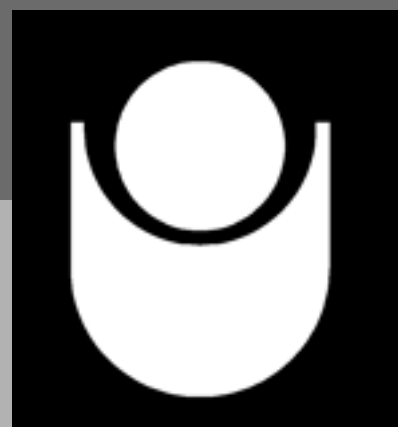



РАЗПРЕДЕЛЕНИЕ НА КОТА+13,25 М 1:250

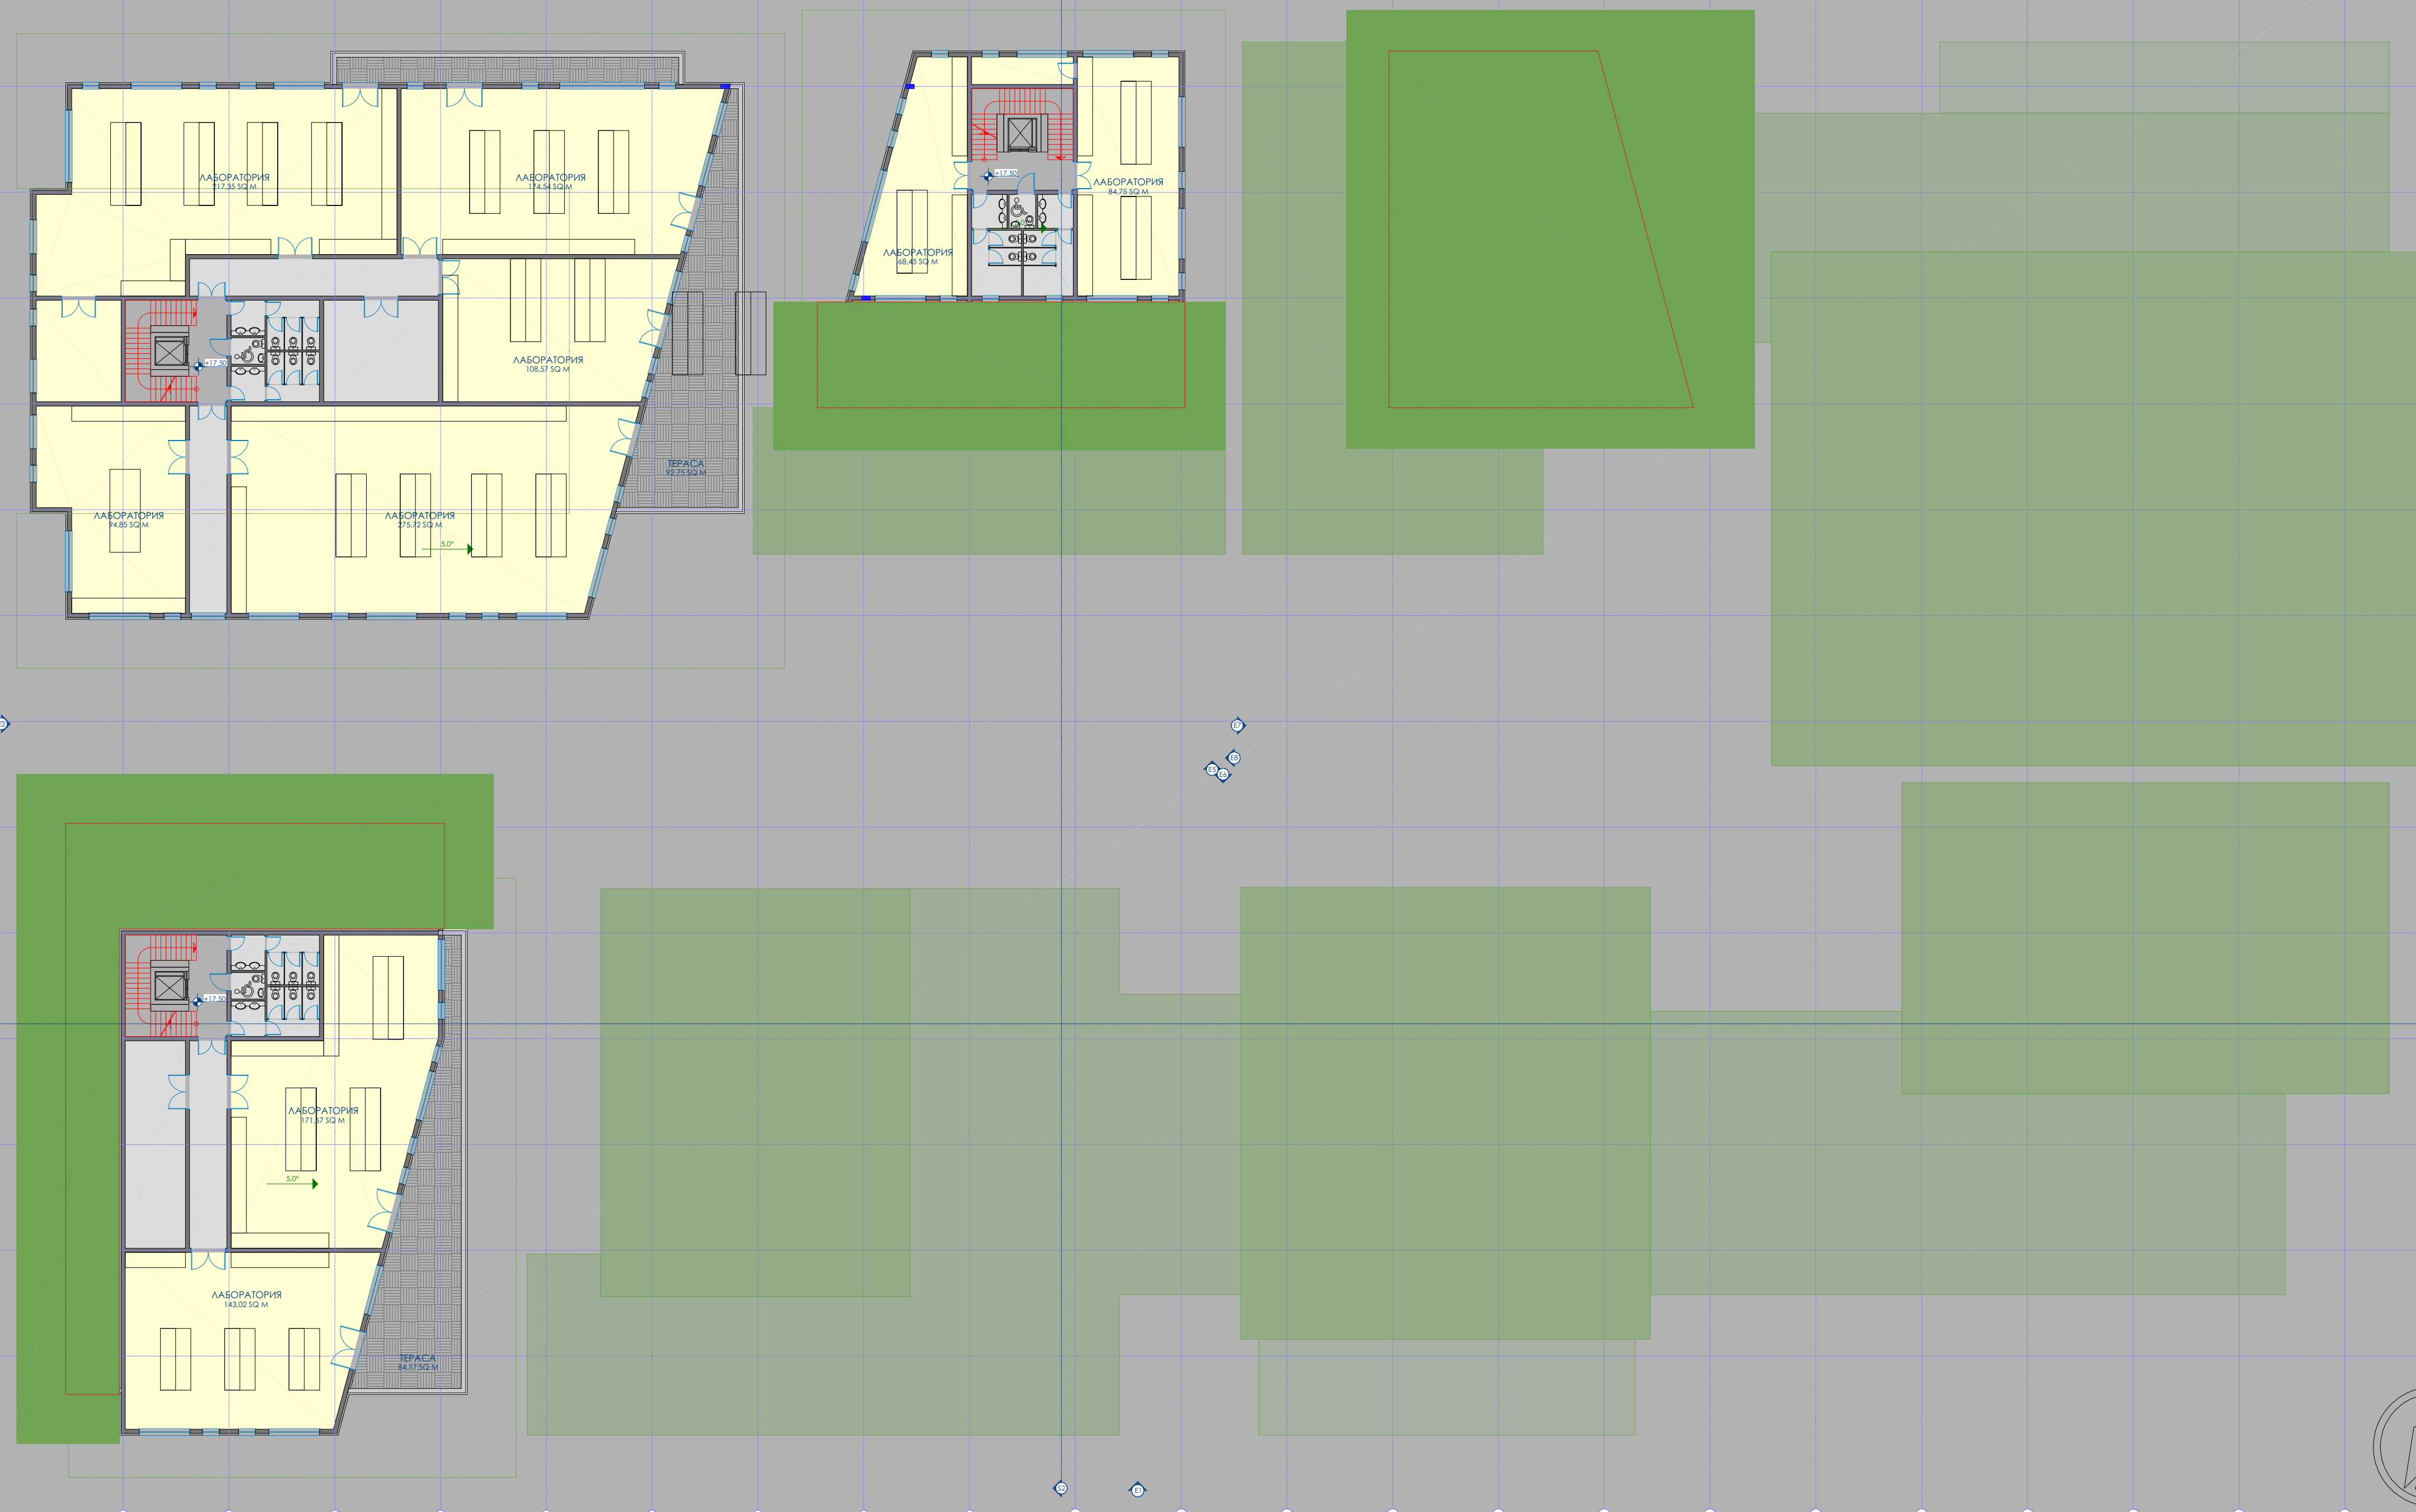


РАЗПРЕДЕЛЕНИЕ НА КОТА+17,50 М 1:250






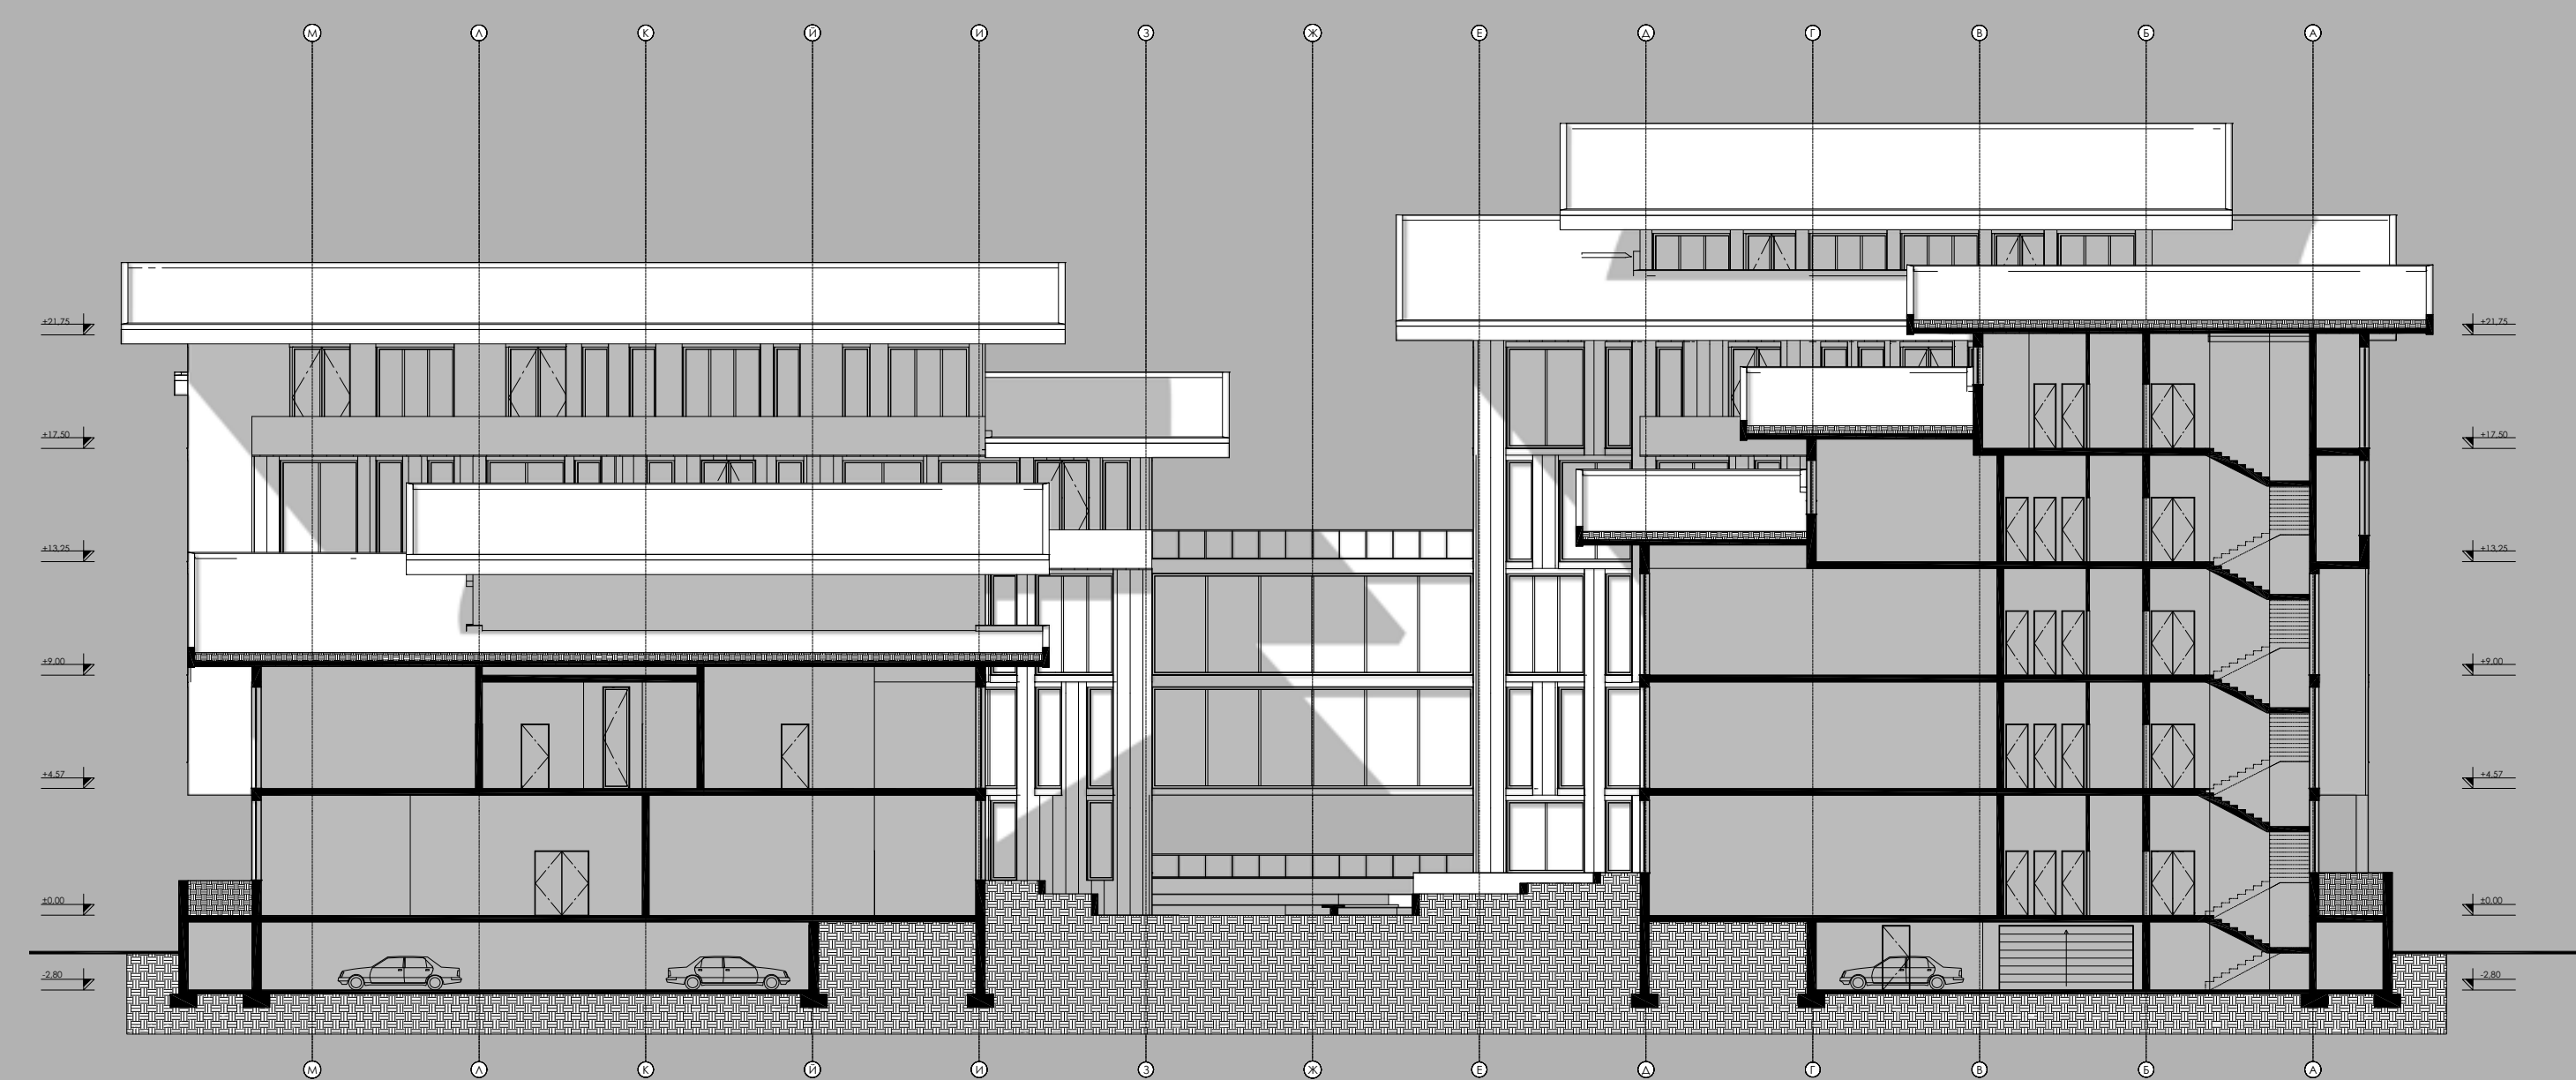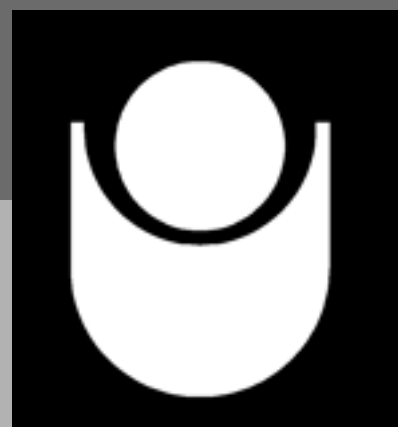

РАЗРЕЗ-S2 М 1:250

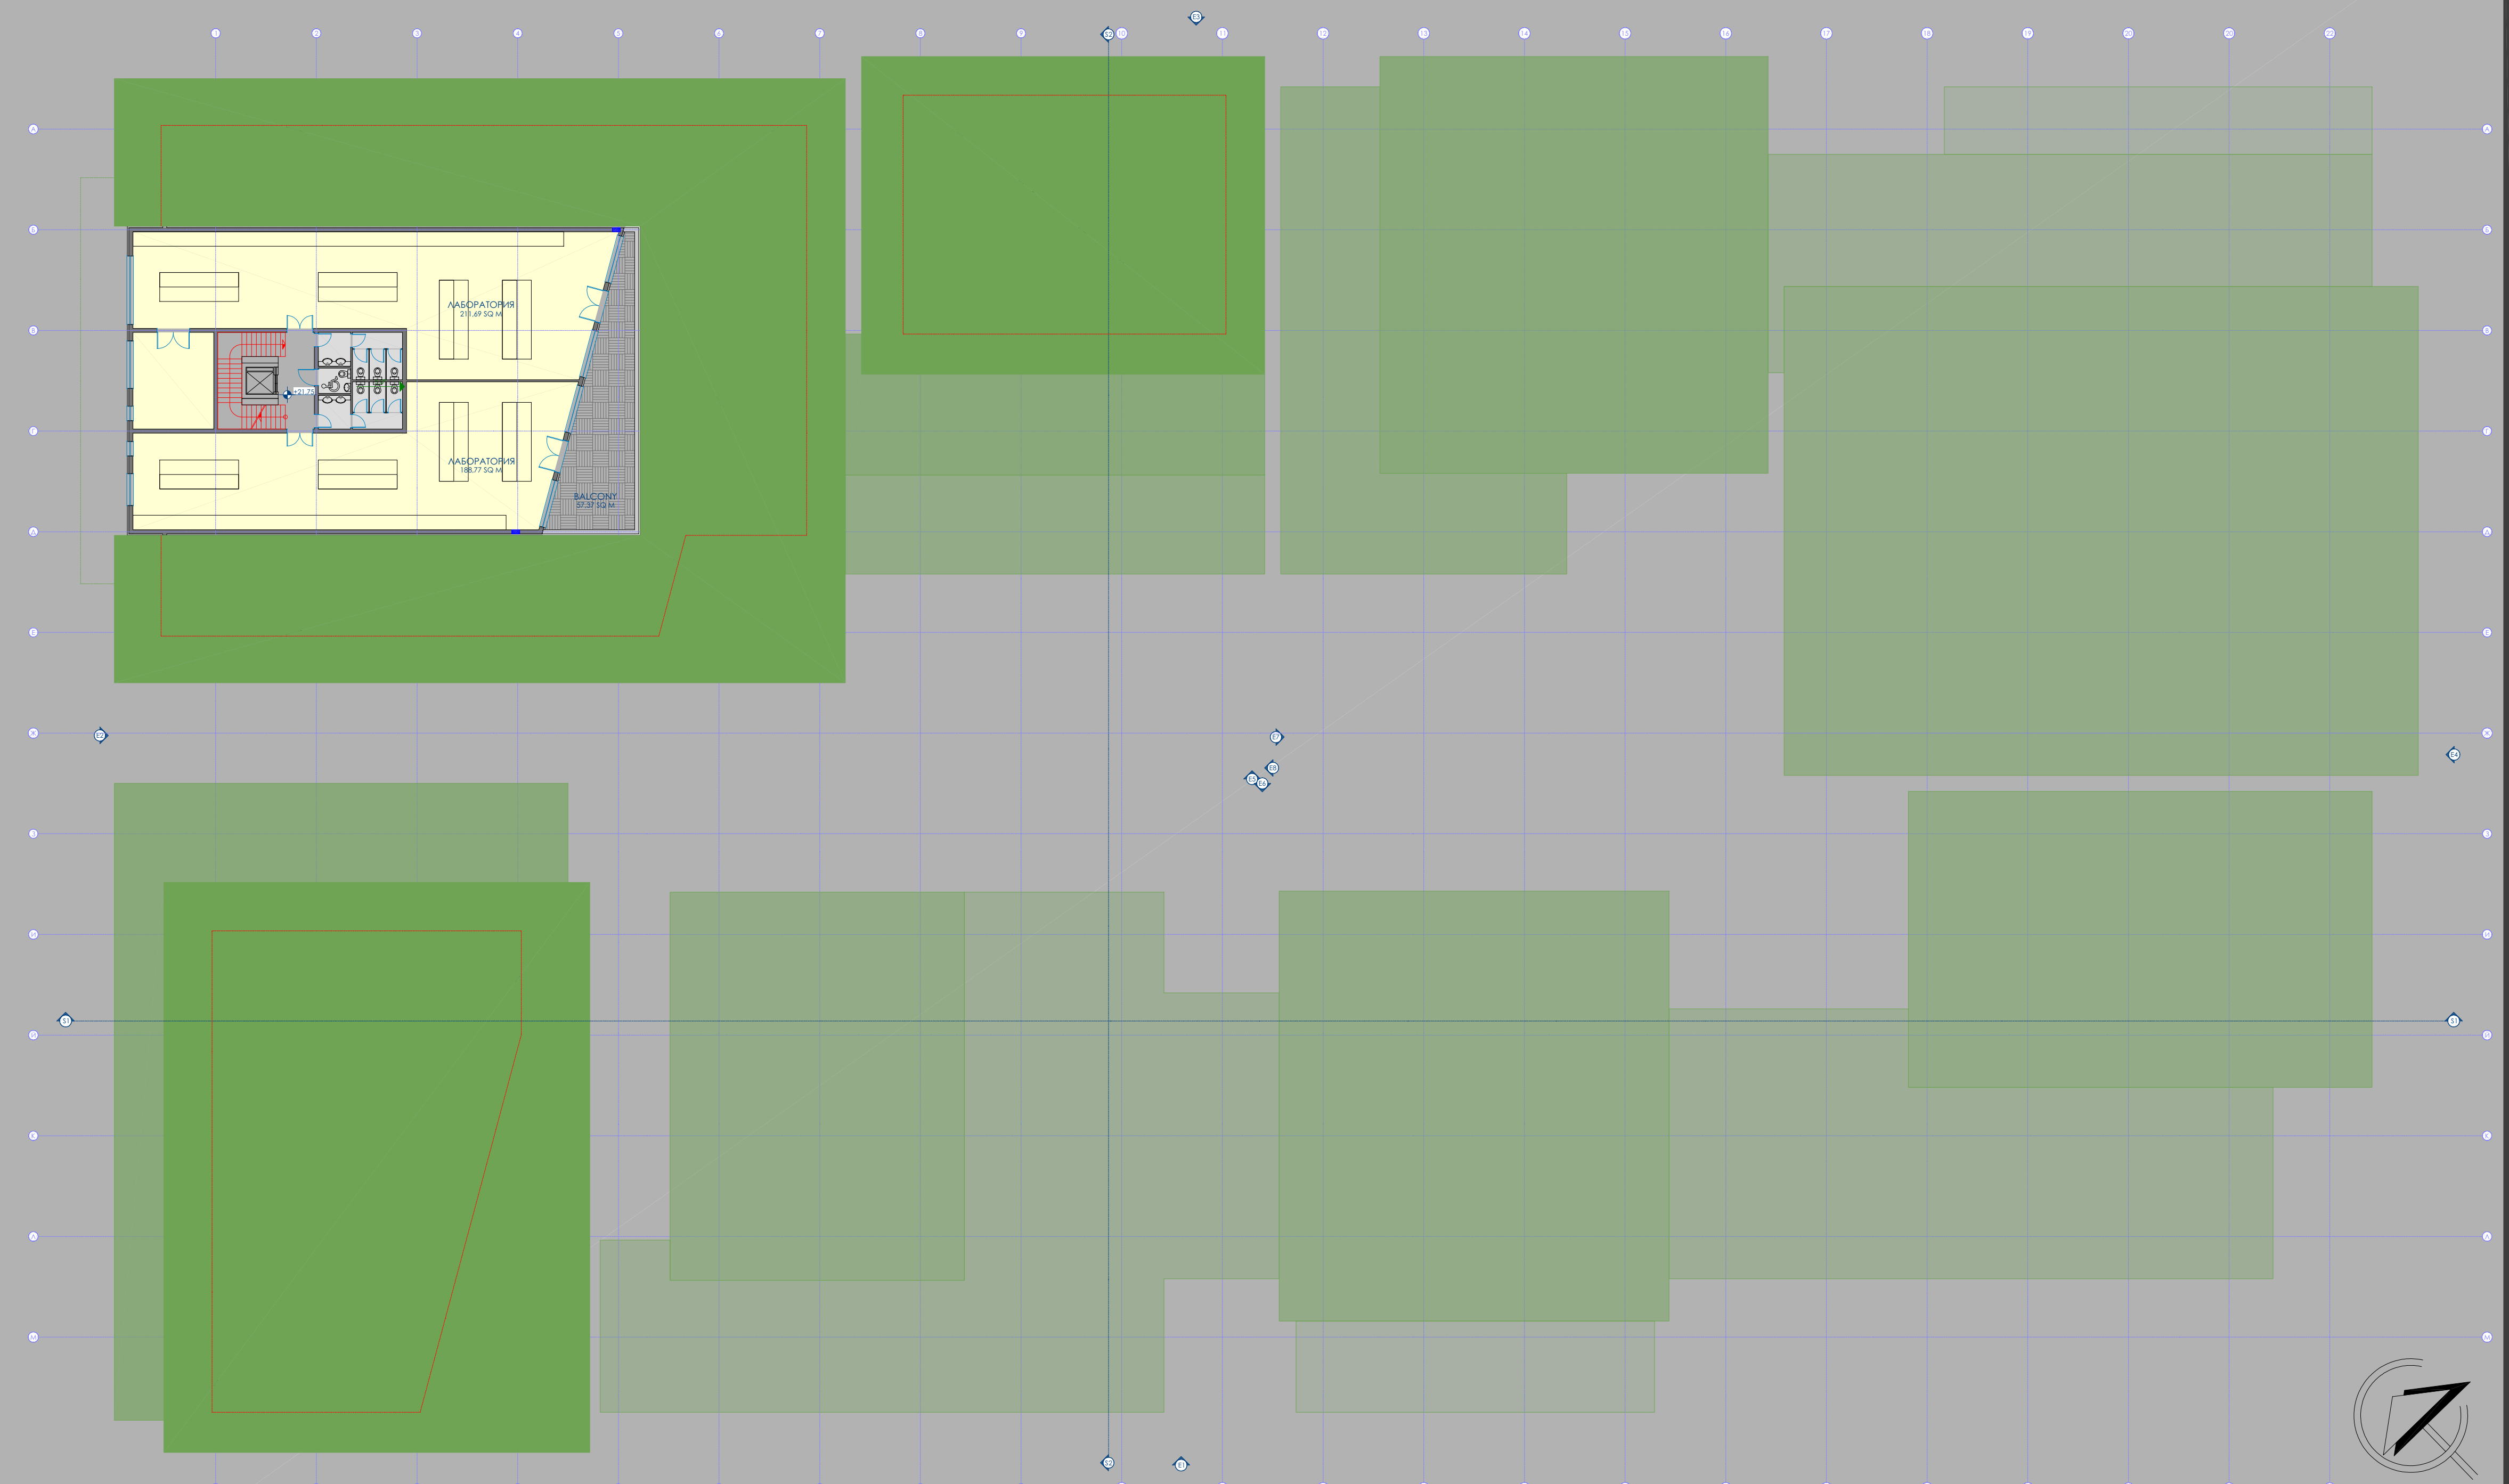

РАЗПРЕДЕЛЕНИЕ НА КОТА+21,75 М 1:250

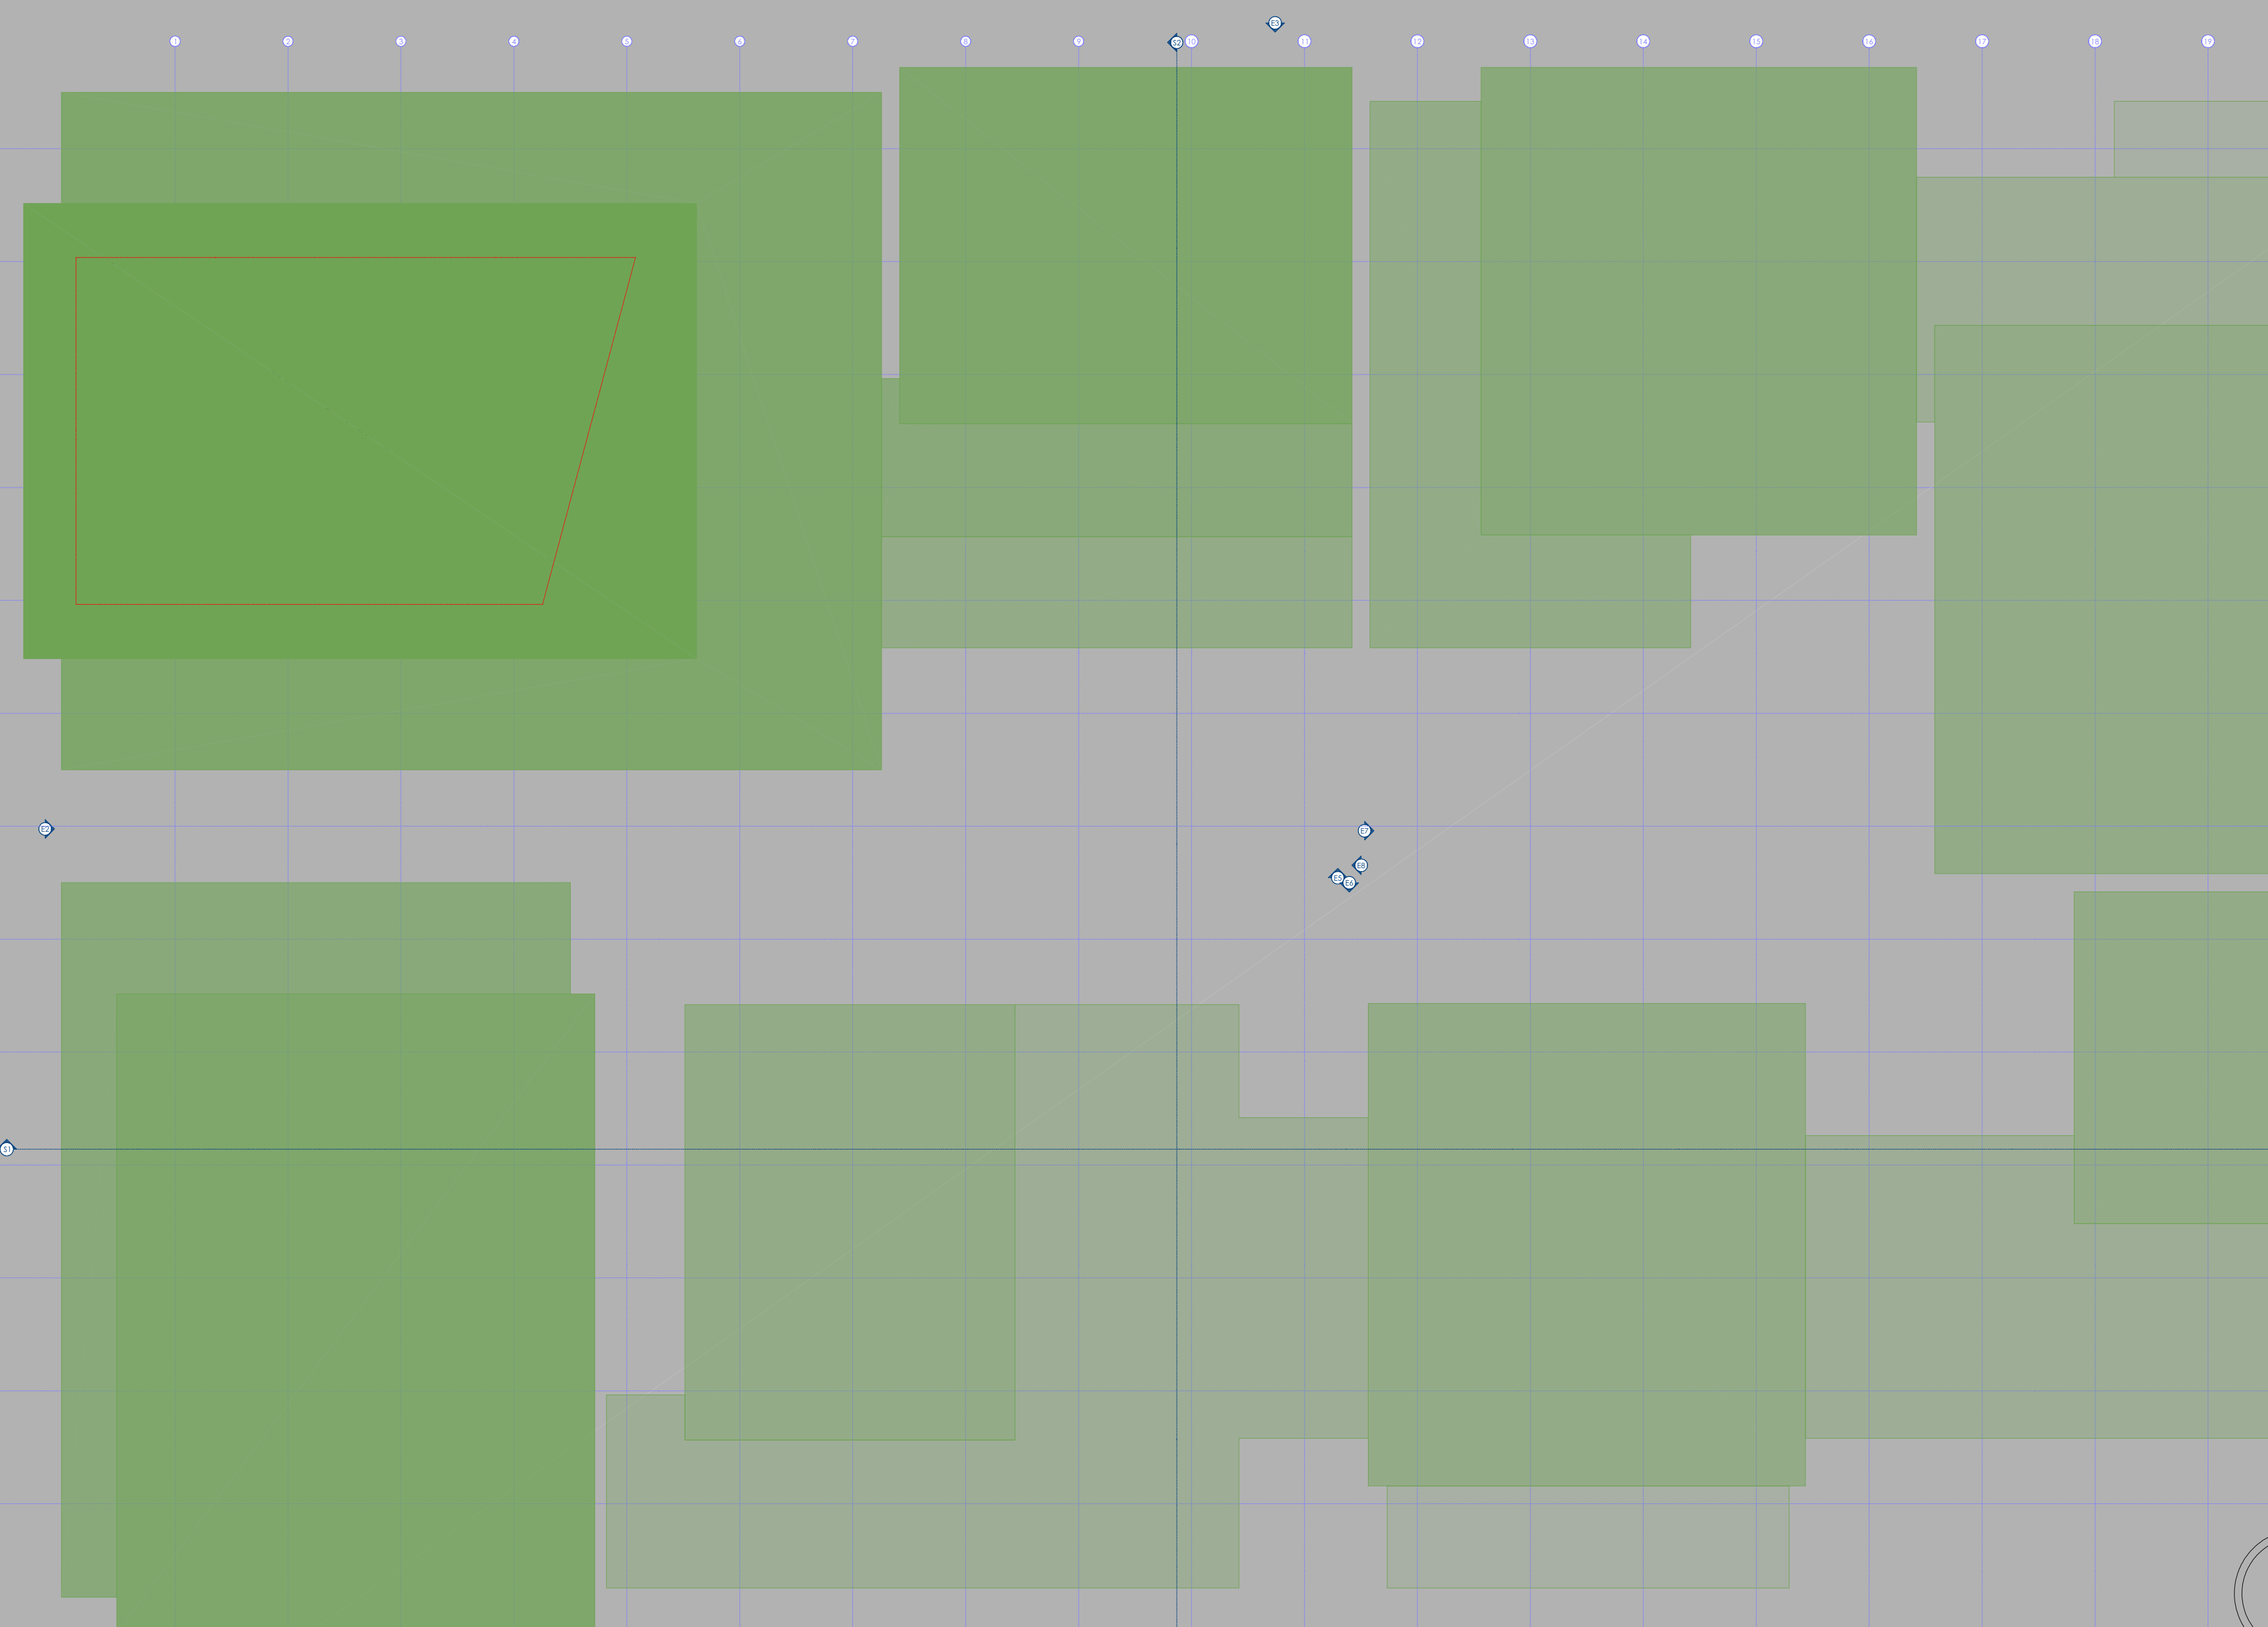


ПЛАН ПОКРИВ М 1:250



РАЗРЕЗ-S1 М 1:250



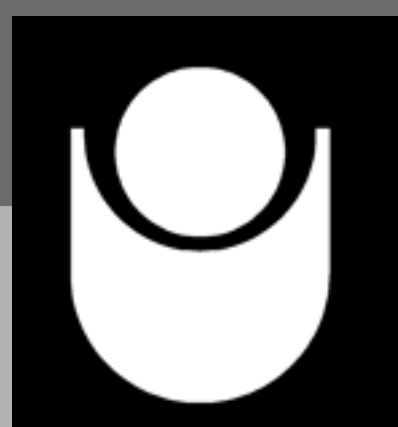

ФАСАДА-Е2, СЕВЕРОЗАПАД М1:250



ФАСАДА-Е1, ЮГОЗАПАД М1:250



ФАСАДА-Е3, СЕВЕРОИЗТОК М1:250



ФАСАДА-Е3, ЮГОИЗТОК М1:250



ФАСАДА И ЧАСТИЧЕН РАЗРЕЗ-Е7 М1:250



ФАСАДА И ЧАСТИЧЕН РАЗРЕЗ-Е5 М1:250



ФАСАДА И ЧАСТИЧЕН РАЗРЕЗ-Е6 М1:250



ФАСАДА И ЧАСТИЧЕН РАЗРЕЗ-Е8 М1:250